


# MAKİNE-EKİPMAN YERLEŞİM PLANI

MUSAB EDER ÇİFTLİĞİ KANATLI (ETLİK PİLİÇ) KÜMESİ

KOCAELİ İLİ KARAMÜRSEL İLÇESİ İNEBEYLİ MAHALLESİ ADA:138 PARSEL:17

Ölçek 1:300 · Kümes A ve B blok özdeşdir

İç ölçü 78,55 x 13,50 m = 1.060,42 m<sup>2</sup>

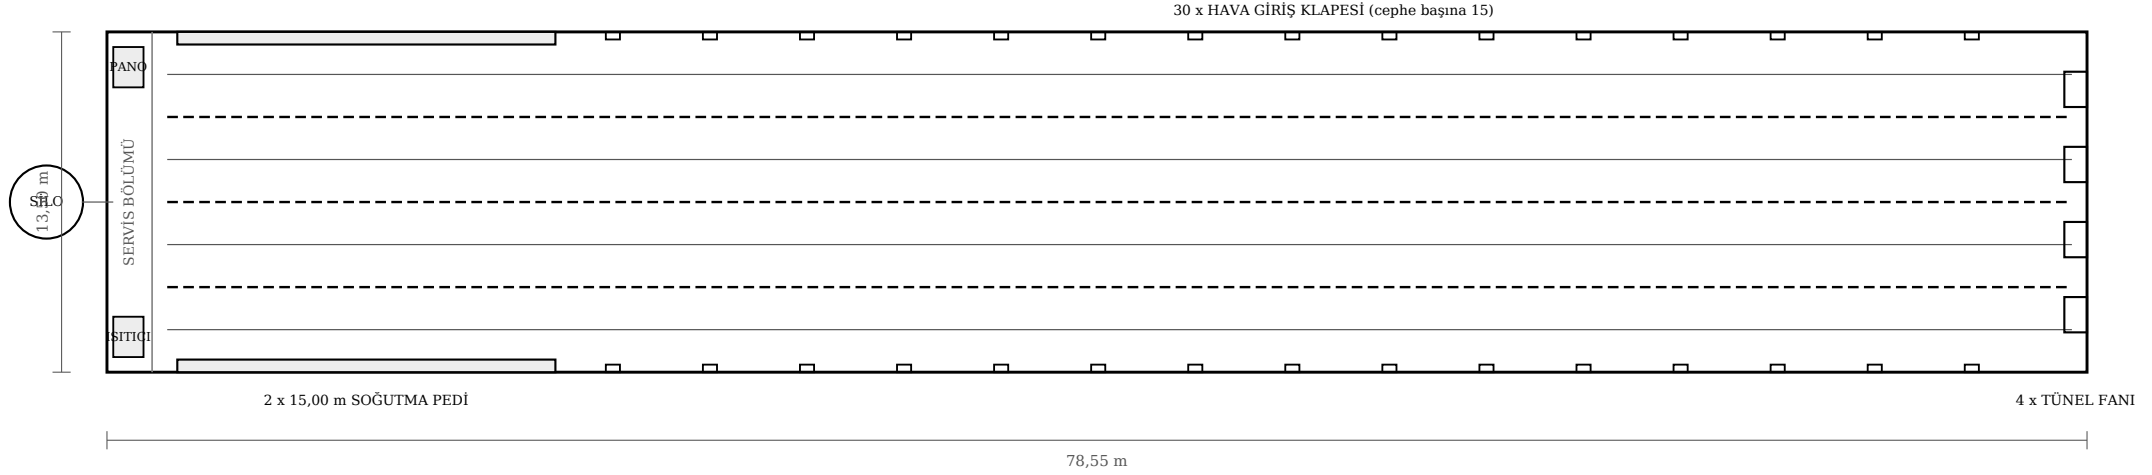

## Kümes başına makine-ekipman

|                      |         |                             |             |                         |        |
|----------------------|---------|-----------------------------|-------------|-------------------------|--------|
| Yemleme sistemi      | 3 hat   | Sulama sistemi (nipel)      | 4 hat       | Tünel havalandırma fanı | 4 adet |
| Hava giriş klapesi   | 30 adet | Soğutma pedi                | 2 x 15,00 m | Yem silosu              | 1 adet |
| Kümes kontrol panosu | 1 adet  | Sıcak hava üretici (ısıtma) | 1 adet      |                         |        |

Adetler makine-ekipman teknik şartnamesi (07), ihtiyaç listesi (12), proforma istek listesi (37) ve teknik proje (44) ile aynıdır; hepsi tek kaynaktan üretilir.

Bu çizim ekipmanın yerleşim düzenini ve adedini gösterir; mimari pafta yerine geçmez. Proje müellifi onaylı paftaya bu düzeni işler.