KELEŞOĞLU MİMARLIK

tel: 0544 453 59 61 email:keleSoglumimarlik@gmail.com adres: ilimtepe mah. 18. sokak no:2 körfez/kocaeli

MUSAB EDER - MİMARİ PROJESİ

Ruhsat Veren Kurum: KARAMÜRSEL BELEDİYESİ
İli: KOCAELİ
İlçesi: KARAMÜRSEL
Ruhsat Veriliş Maksadı: YENİ YAPI
Ruhsat Tarihi
Ruhsat Numarası
Köyü/Mah.: İNEBEYLİ
Pafta No.: G23-D-11-B-3
Ada No.: 138
Parsel No.: 17
İmar Durumu Tarihi
İmar Durumu Numarası
Isınma Türü
Yakıt Türü
Tapu Tescil Belgesi Veren Kurum
Tapu Tescil Belgesi Tarihi
Tapu Tescil Belgesi Numarası

YAPI SAHİBİNİN	YAPI MÜTEAHHİDİNİN
Adı Soyadı / Unvanı: MUSAB EDER	Adı Soyadı / Unvanı
	Kurum Sicil numarası
Bağlı Olduğu Vergi Dairesi	Bağlı Olduğu Vergi Dairesi
Vergi Dairesi Sicil Numarası	Vergi Dairesi Sicil Numarası
Adresi: KARAMÜRSEL/KOCAELİ	Adresi

İNŞAAT ALANI		Ünite Sayısı	Yüz Ölçümü	Yol Seviyesi Altında Kat Sayısı	Yol Seviyesi Üstünde Kat Sayısı	Toplam Kat Sayısı	Yapının Yüksekliği	1 m² sinin Maliyeti	Yapı Sınıfı	Yapı Grubu
KÜMES A BLOK	ZEMİN KAT		1106 m²	0	1	1	4.50 m		2	A
	1. KAT									
	TOPLAM		1106 m²							
KÜMES B BLOK	ZEMİN KAT		1106 m²	0	1	1	4.50 m		2	A
	1. KAT									
	TOPLAM		1106 m²							
GÜBRE ÇUKURU	BODRUM KAT		115 m²	1	0	1	2.70 m		1	B
	TOPLAM		115 m²							
ÖLÜ ATMA ÇUKURU	BODRUM KAT		18 m²	1	0	1	3.00 m		1	B
	TOPLAM		18 m²							
BAKICI EVİ	BODRUM KAT									
	ZEMİN KAT		120 m²	0	2	2	5.76 m		3	A
	1. KAT		120 m²							
	TOPLAM		240 m²							
FOSEPTİK	BODRUM KAT		4 m²	1	0	1	2.50 m		1	B
	TOPLAM		4 m²							
YAĞMUR SUYU DEPOSU	BODRUM KAT		9 m²	1	0	1	3.00 m		1	C
	TOPLAM		9 m²							
SİLO	BODRUM KAT	2	8.41 m²	0	1	1	5.00 m		1	B
	TOPLAM		16.82 m²							
SU DEPOSU	BODRUM KAT		12 m²	1	0	1	3.00 m		1	C
	TOPLAM		12 m²							
	GENEL TOPLAM		2626.82 m²							

İnşaatın Toplam Maliyeti (Arsa Hariç)
Ait Olduğu Yıl: 2026
Yapının Arsa Değeri
Toplam Maliyet (Arsa Dahil)
İskeletin Cinsi
İskeletin Dolgu Maddesi
Yığma Yapının Cinsi

UYARI !

İşe başlamadan evvel bütün ölçüleri şantiyede kontrol edip,farkları ilgililere bildiriniz.

5846 sayılı fikir ve sanat eserleri yasası gereğince bu tasarıma ait bütün haklar proje müellifi mimara aittir.

Bu projedeki taşıyıcı sistem mimari tasarımla bir bütündür. Proje müellifi mimarın haberi ve onayı olmadan projede, projedeki taşıyıcı sistemde ve yapı üzerinde değişiklik yapılamaz, kopya edilemez ve çoğaltılamaz.

MİMAR KAŞE/İMZA

RUHSAT EKİ PROJELER		
BRANŞI	ADI SOYADI	Oda sicil no. Büro tescil no.
Mimari Proje	İNCİLAY EZGİ KELEŞOĞLU	91996 41-0987
Statik Proje		
Tesisat Projesi		
Elektrik Projesi		

YAPI DENETİM KURULUŞU

Harice taşınacak kazı miktarı :
Kazı malzemesinin taşınacağı yer :
ŞANTİYE ŞEFİ
Taahhüdü

BELEDİYE ONAYI

MİMARİ PROJENİN;3194 SAYILI İMAR KANUNU VE YÖNETMELİKLERİNE, İMAR DURUMUNA VE RÖPERLİ KROKİSİNE UYGUNLUĞU TARAFIMDAN KONTROL EDİLMİŞTİR.

ODA VİZESİ

MİMARİ

MİMARİ PROJENİN;3194 SAYILI İMAR KANUNU -YÖNETMELİKLERİNE, İMAR DURUMUNA VE RÖPERLİ KROKİSİNE UYGUNLUĞU TARAFIMDAN KONTROL EDİLMİŞTİR.

SN. MUSAB EDER'E AİT KÜMES VE BAKICI EVİ PROJESİ

İLİ:..KOCAELİ
İLÇESİ:..KARAMÜRSEL
BELEDİYESİ:....................................KARAMÜRSEL
MAHALLESİ:.....................................İNEBEYLİ
PAFTASI:.......................................G23-D-11-B-3
ADASI:...138
PARSELİ:.......................................17
ALANI:...7966.67 m²

ARSA ALANI	7966.67 M²	
TAKS	–	
KAKS	0.30 + 0.05	
AZAM? TABAN ALANI (TAKS) –		
	KÜMES(A+B)	BAKICI EV?
AZAM? TABAN ALANI (KAKS)	2390 M²	TABAN MAX: 150 M²
PROJEDE TABAN ALANI	1176 M²	120 M²
PROJEDE KAKS'A DAH?L	2352 M²	120 M²

ÇEKME MESAFELER?	
ÖN BAHÇE	10 M
YAN BAHÇE	5 M
ARKA BAHÇE	5 M

1/25000 Ölçekli nazım imar planı hükümlerinin Tarımsal Niteliği Korunacak Alanlar başlıklı plan hükmünde yer alan hmax 6,50 mt (2 kat), e:0.30 değerini aşmayacak şekilde 6.6.2 maddesinde tanımlanan tarımsal amaçlı yapılar yapılabilir." ifadelerinin, "Tarımsal niteliği korunacak alanlar içerisinde belediyesinin uygun görmesi halinde; ilgili kurum ve kuruluşların taşra teşkilatlarının uygun görüşününalınması ve başka bir amaçla kullanılmayacağı hususunda tesis sahiplerince ilgili idareye noterlikçe tasdikli yazılı taahhütte bulunulması şartıyla, hmax 6,50 mt (2 kat), inşaat alanı katsayısı % 30 değerini aşmayacak şekilde 6.6.2maddesinde tanımlanan tarımsal amaçlı yapılarla birlikte inşaat alanı katsayısı %5'den fazla olmayan ve tabanda 75 m² ve 2 kat'ı geçmeyen tarımsal amaçlı bağ evi yapılabilir."

Resmî Gazete'de yayımlanan 04.04.2026 tarihli Tarım Arazilerinin Korunması ve Kullanılmasına Dair Yönetmeliğe göre; "Tarımsal niteliği korunacak alanlar içerisinde; belediyesinin uygun görmesi halinde, ilgili kurum ve kuruluşların taşra teşkilatlarının uygun görüşünün alınması ve başka bir amaçla kullanılmayacağı hususunda tesis sahiplerince ilgili idareye noterlikçe tasdikli yazılı taahhütte bulunulması şartıyla, yönetmeliğin 11.9 maddesinde tanımlanan kanatlı hayvancılık tesisleri (kümes) yapılabilir. Bu kapsamda; kanatlı hayvancılık tesisinin kapalı alanına bağlı olarak, 750 m² ile 1500 m² arasında olması durumunda taban alanı 75 m² ve toplam inşaat alanı 150 m²'yi geçmeyen, 1500 m²'nin üzerinde olması durumunda ise taban alanı 150 m² ve toplam inşaat alanı 300 m²'yi geçmeyen bakıcı evi yapılabilir.

TAKS HESABI= BAKICI EVİ TABAN ALANI < 150 M²
BAKICI EVİ TABAN ALANI = 120 M² < 150 M² OLDUĞUNDAN TAKS UYGUNDUR.

KAKS HESABI = KÜMES ALANI + BAKICI EVİ ALANI = PARSEL ALANI X (0.30) + PARSEL ALANI X (0.05)
7966.67 X (0.30) + 7966.67 X (0.05) = 2390.0 M² + 398.33 M² = 2788.33 M²

KÜMES (A) 1106.00 M²
KÜMES (B) 1106.00 M²
TOPLAM = 2212 M² < 2390 M² OLDUĞUNDAN KAKS UYGUNDUR.

BAKICI EVİ (ZEMİN KAT) 120 M²
BAKICI EVİ (1.KAT) 120 M²
TOPLAM = 240 M² < 398.33 M² OLDUĞUNDAN KAKS UYGUNDUR.

TOPLAM =2212 M² + 240 M² < 2390 M² +240 M² = 2452 M² < 2788.33 M² OLDUĞUNDAN TOPLAM KAKS UYGUNDUR.

TOPLAM BOZULAN ALAN TABLOSU
A–)KÜMES (A BLOK) : 1106 M²
B–)KÜMES (B BLOK) : 1106 M²
C–)GÜBRE ÇUKURU : 115 M²
D–)ÖLÜ ATMA ÇUKURU : 18 M²
E–)BAKICI EVİ : 120.00 M²
F–)FOSEPTİK : 4.00 M²
G–)YAĞMUR SUYU DEPOSU : 9.00 M²
H–)SU DEPOSU : 12.00 M²
I–)TESİS İÇİ YOL : 745.57 M²

1–)SİLO (A): 8.41 M²
2–)SİLO (B): 8.41 M²

TOPLAM : 3252.39 M²

±0.00 KOTLARI
A–)KÜMES (A BLOK)
±0.00 KOTU =180.45+181.57+180.59+179.26/4= 180.46 ort. kot
B–)KÜMES (B BLOK)
±0.00 KOTU =181.71+183.19+180.75+181.90/4= 181.88 ort. kot
C–)GÜBRE ÇUKURU
±0.00 KOTU =183.59+184.01+183.16+182.87/4= 183.40 ort. kot
D–)ÖLÜ ATMA ÇUKURU
±0.00 KOTU =183.64+183.71+183.38+183.46/4= 183.54 ort. kot
E–)BAKICI EVİ
±0.00 KOTU =188.02+188.18+186.79+186.87+186.55+186.26/6= 187.11 ort. kot
F–)FOSEPTİK
±0.00 KOTU =188.33+188.40+188.66+188.58/4= 188.49 ort. kot
G–)YAĞMUR SUYU DEPOSU
±0.00 KOTU =180.38+180.44+180.25+180.29/4= 180.34 ort. kot
H–)SU DEPOSU
±0.00 KOTU =179.99+180.15+180.35+180.21/4= 180.17 ort. kot

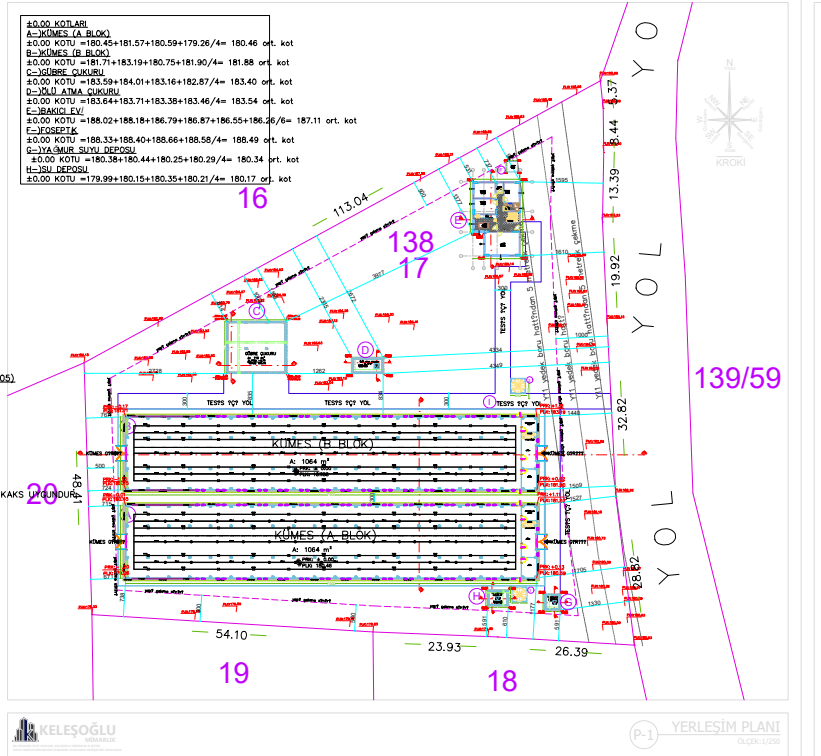

KÜMES A VE B BLOK

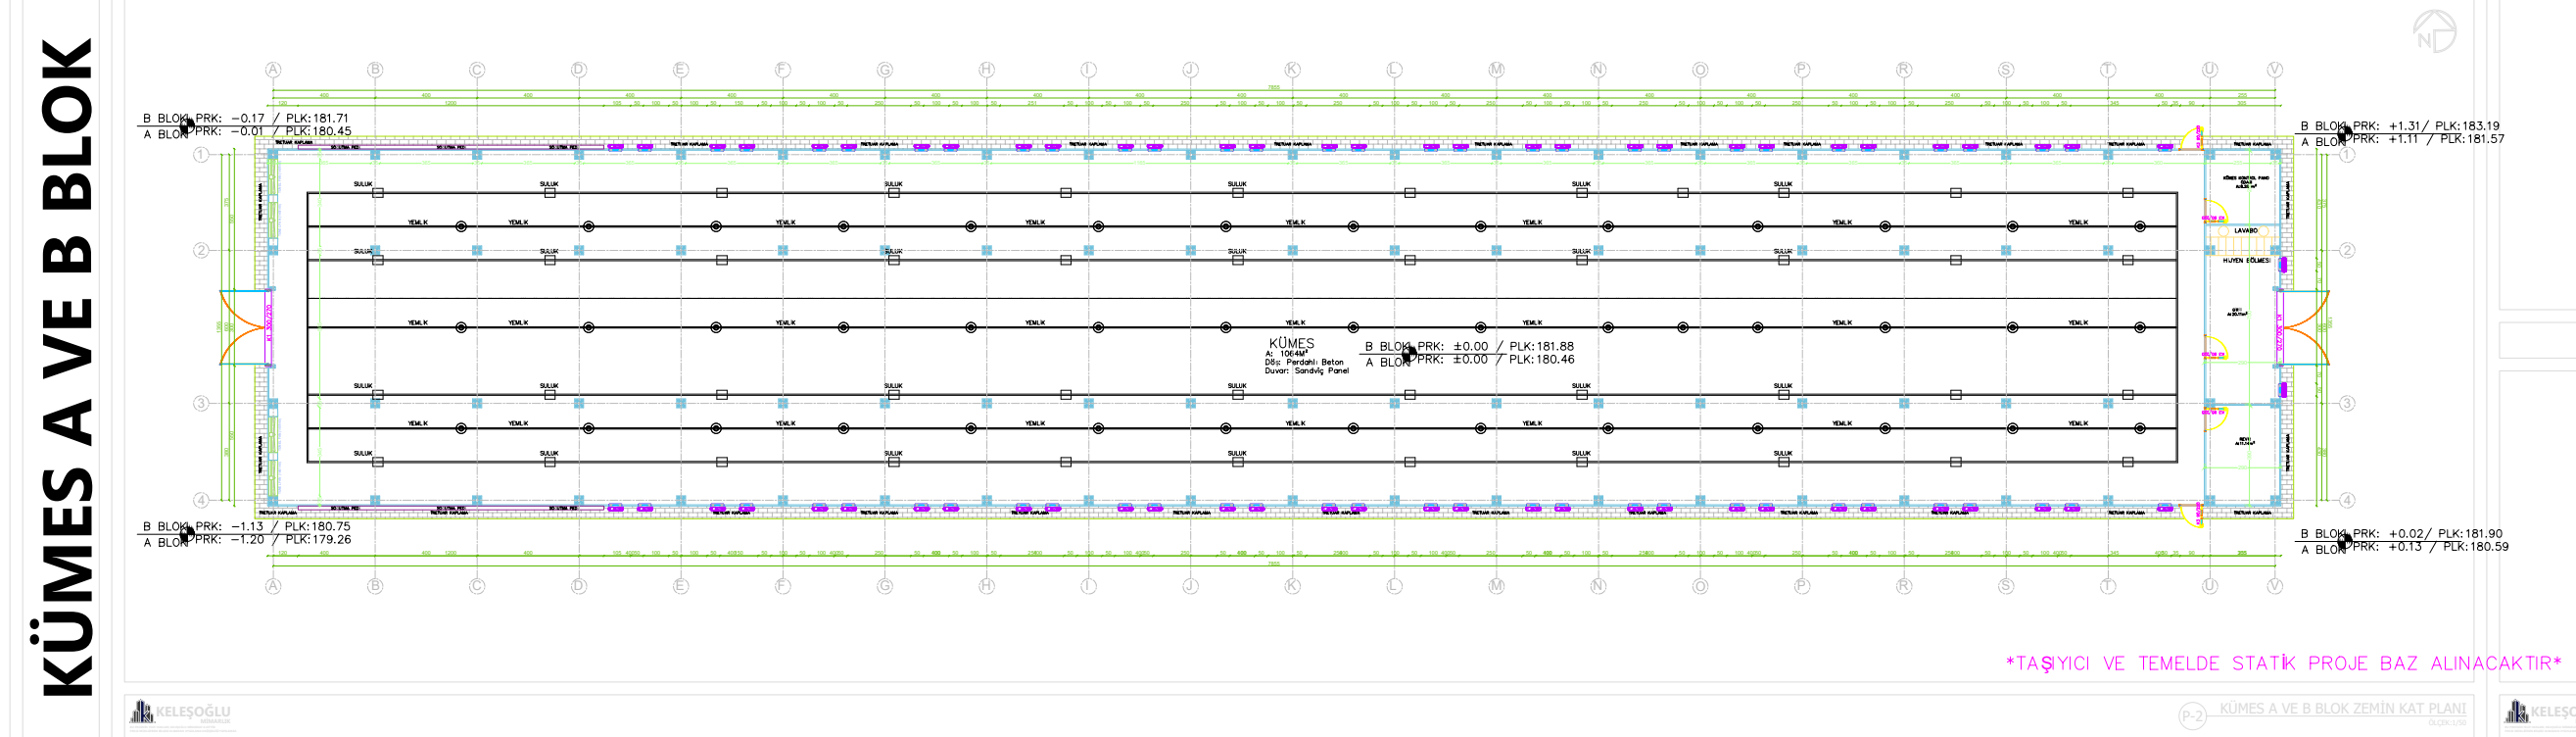
B BLOK PRK: –0.17 / PLK:181.71
A BLOK PRK: –0.02 / PLK:180.43
KÜMES
B BLOK PRK: ±0.00 / PLK:181.88
A BLOK PRK: ±0.00 / PLK:180.46
TAŞIYICI VE TEMELDE STATİK PROJE BAZ ALINACAKTIR
P-2 KÜMES A VE B BLOK ZEMİN KAT PLANI
ÖLÇEK:1/50

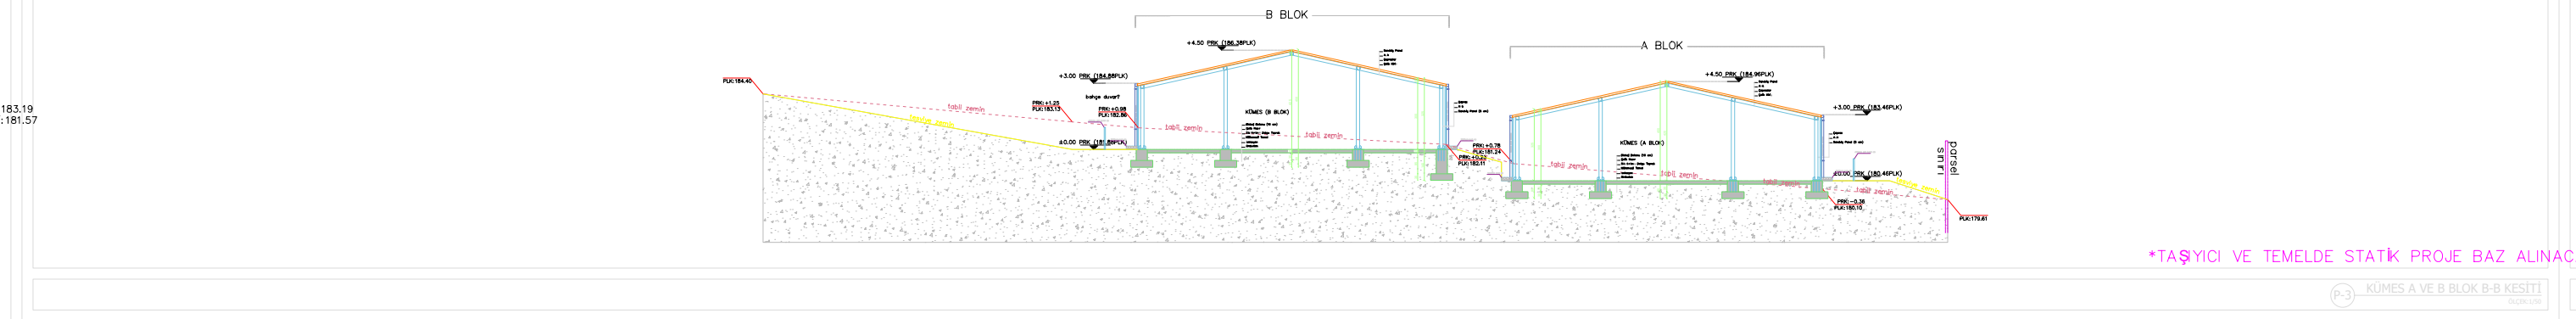

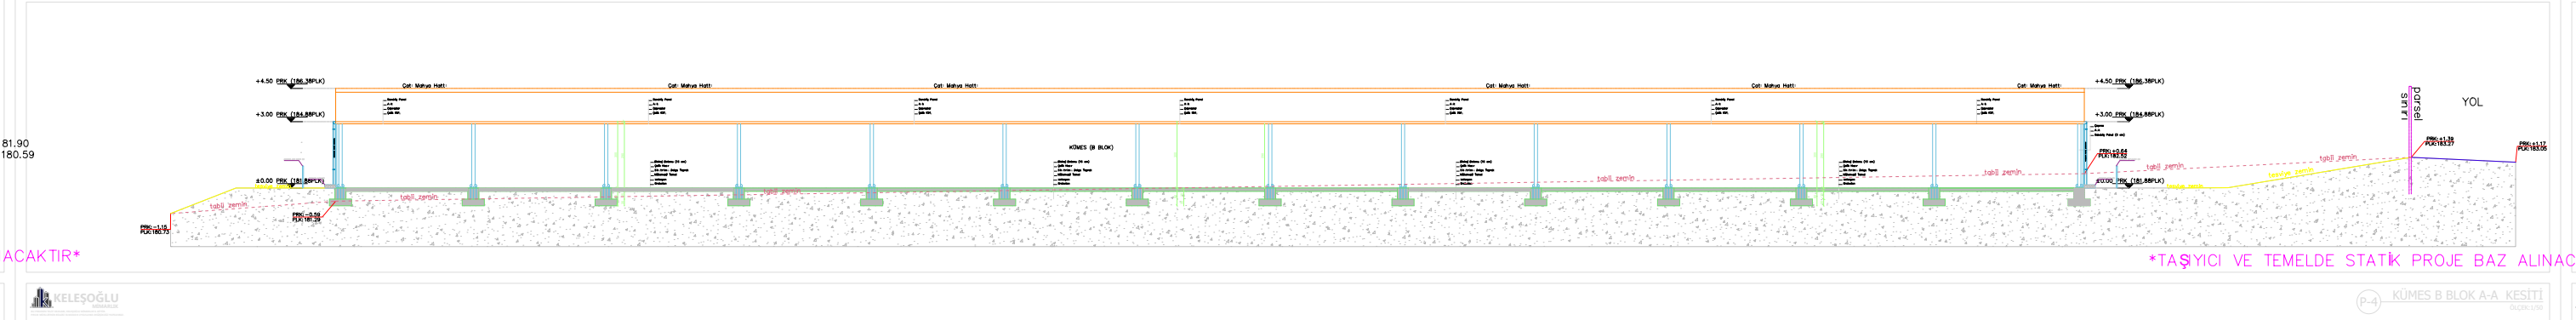
YOL
TAŞIYICI VE TEMELDE STATİK PROJE BAZ ALINACAKTIR
P-4 KÜMES B BLOK A-A KESİTİ
ÖLÇEK:1/50

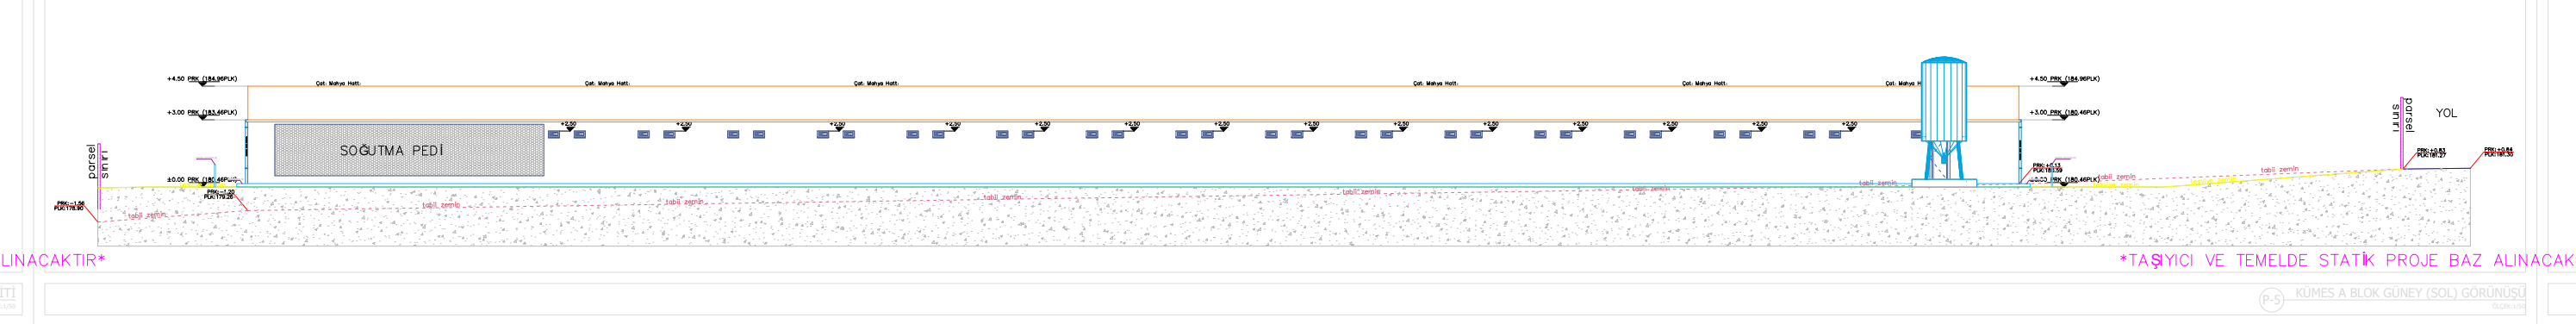

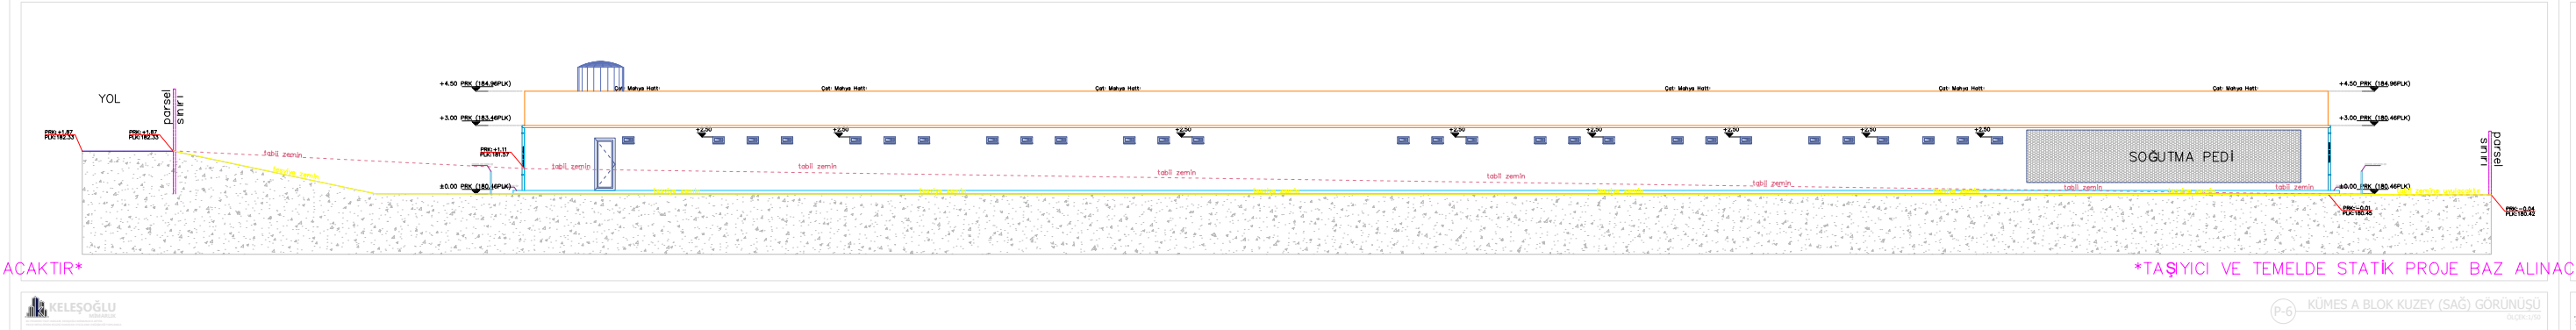
YOL
SOĞUTMA PEDİ
TAŞIYICI VE TEMELDE STATİK PROJE BAZ ALINACAKTIR
P-6 KÜMES A BLOK KUZEY (SAĞ) GÖRÜNÜŞÜ
ÖLÇEK:1/50

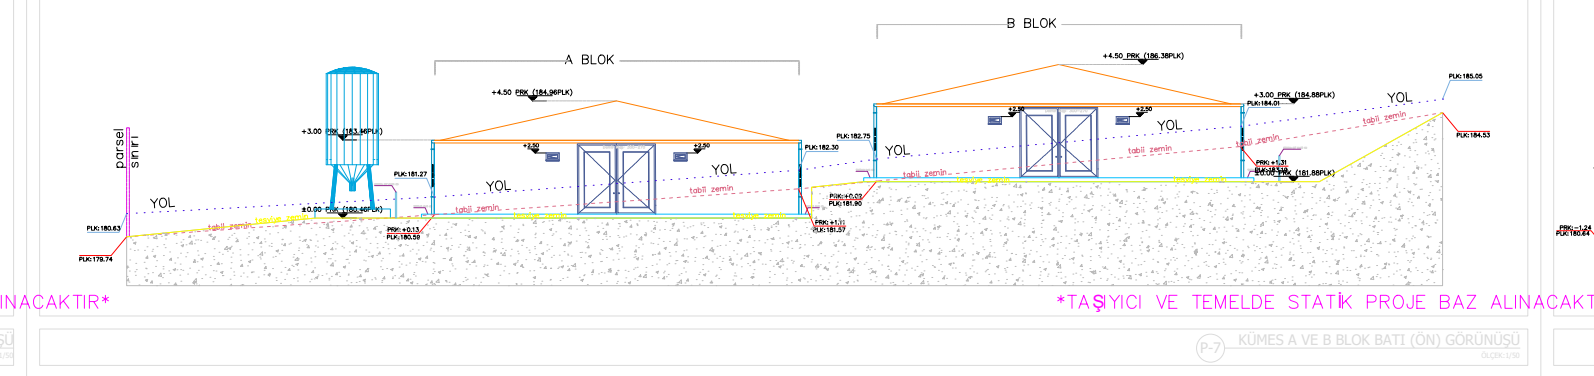

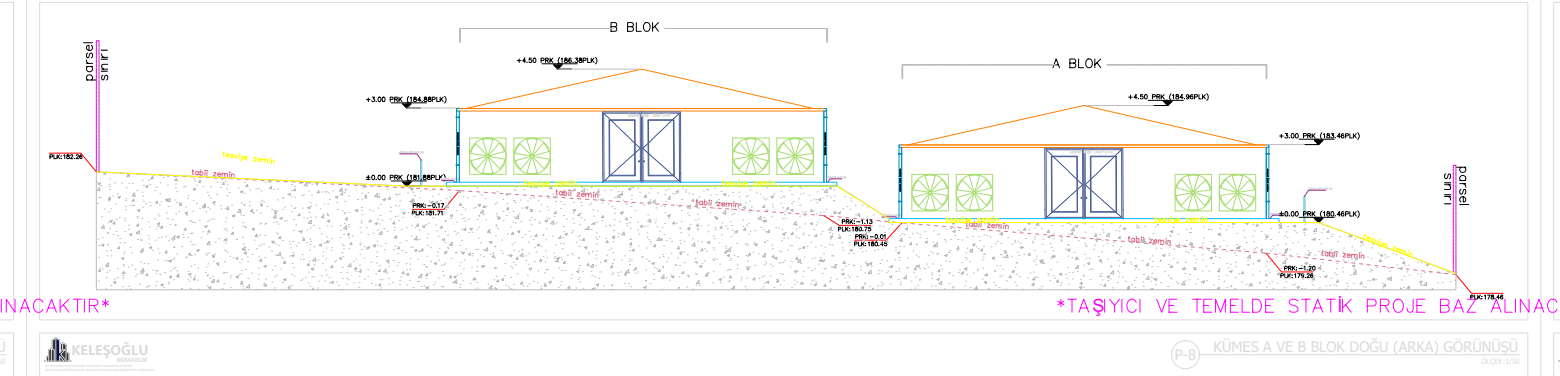
B BLOK
A BLOK
TAŞIYICI VE TEMELDE STATİK PROJE BAZ ALINACAKTIR
P-8 KÜMES A VE B BLOK DOĞU (ARKA) GÖRÜNÜŞÜ
ÖLÇEK:1/50

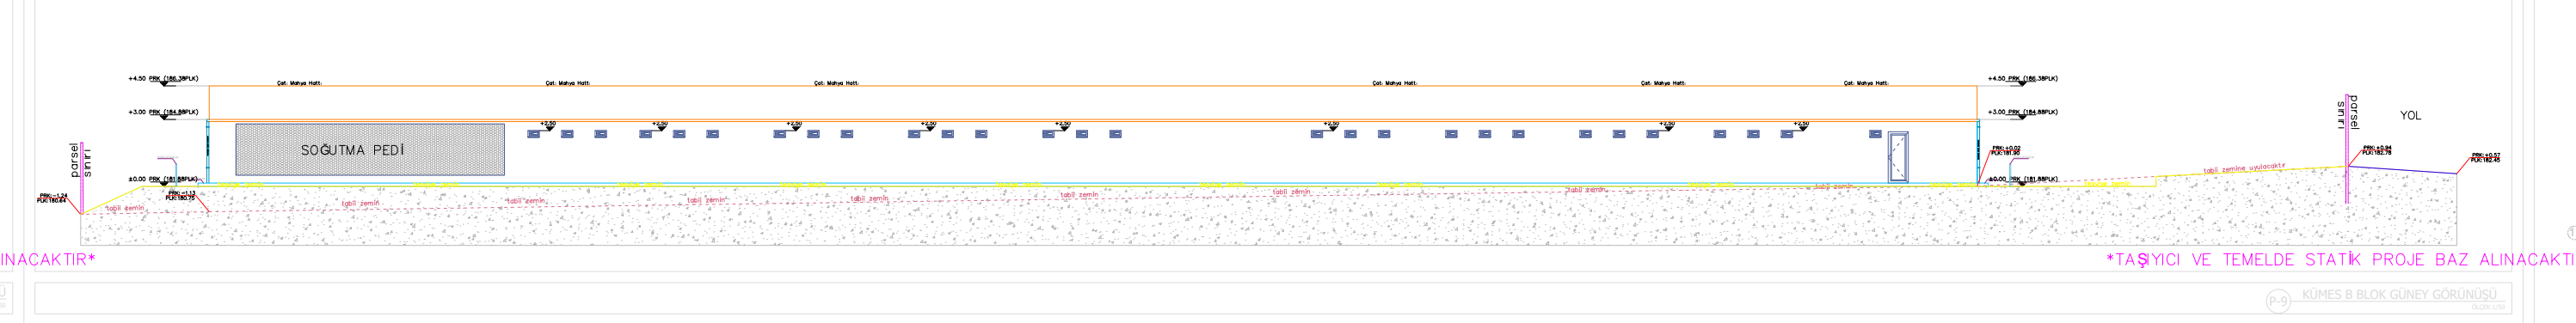

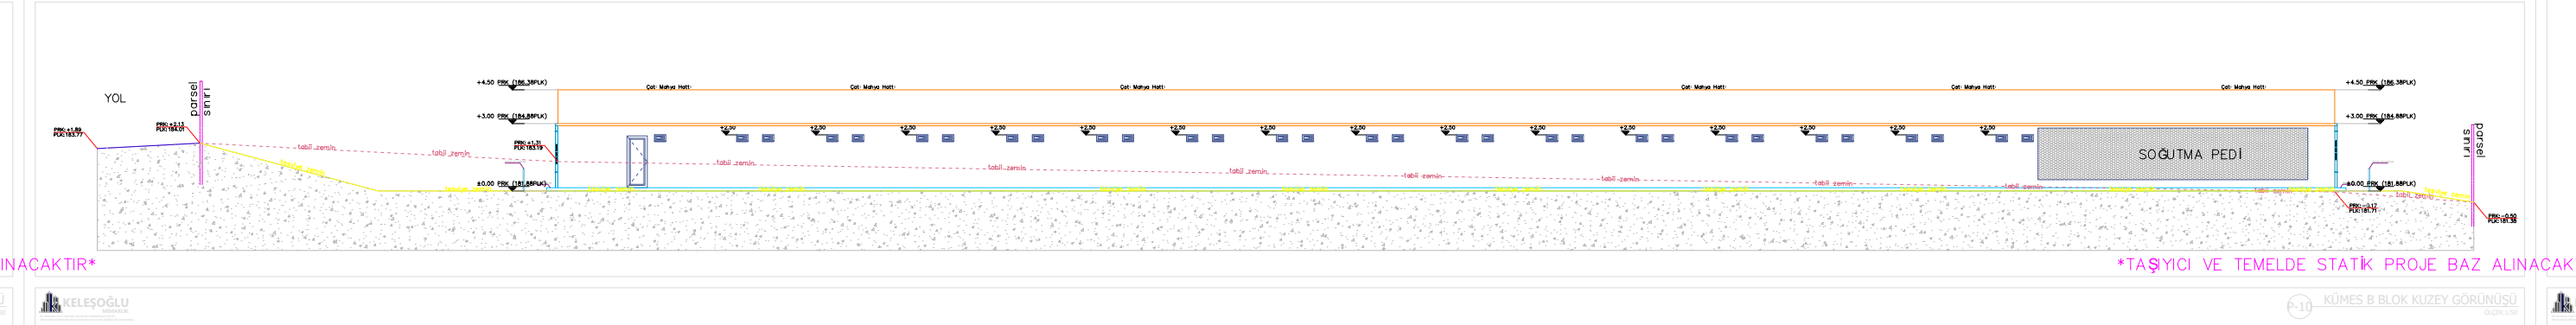
YOL
SOĞUTMA PEDİ
TAŞIYICI VE TEMELDE STATİK PROJE BAZ ALINACAKTIR
P-10 KÜMES B BLOK KUZEY GÖRÜNÜŞÜ
ÖLÇEK:1/50

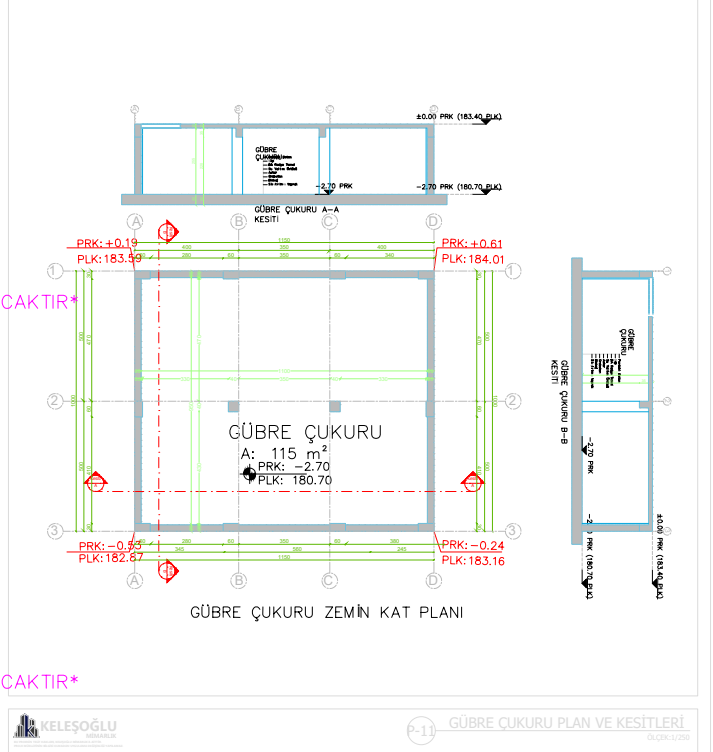
GÜBRE ÇUKURU
A: 115 m²
PRK: –2.70
PLK: 180.70
GÜBRE ÇUKURU ZEMİN KAT PLANI
P-11 GÜBRE ÇUKURU PLAN VE KESİTLERİ
ÖLÇEK:1/250

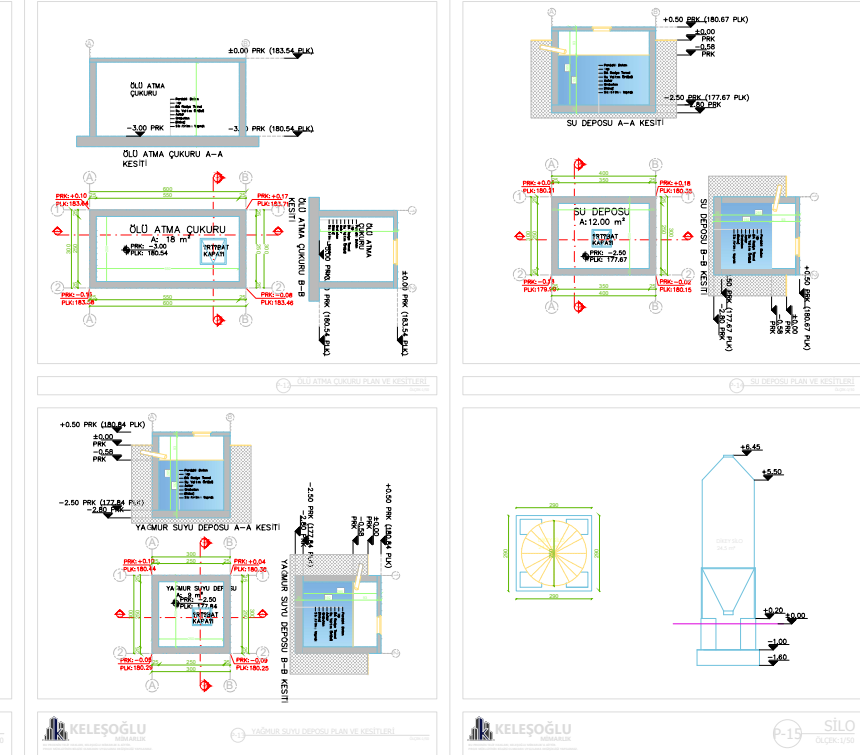

BAKICI EVİ

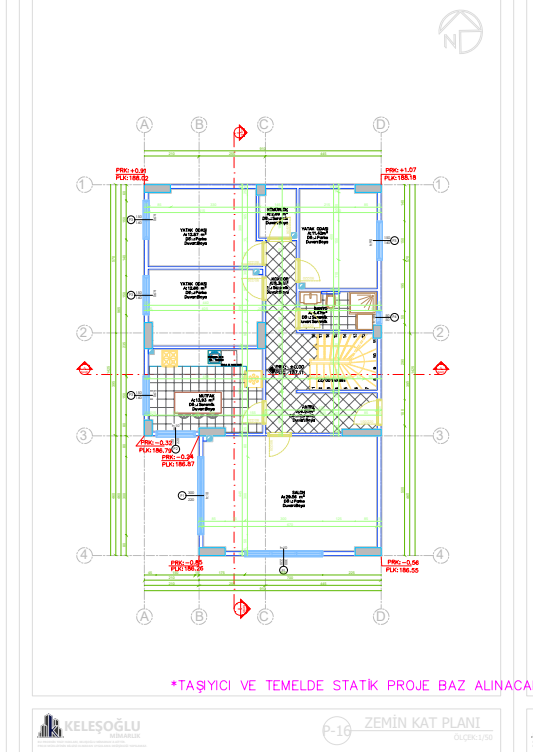

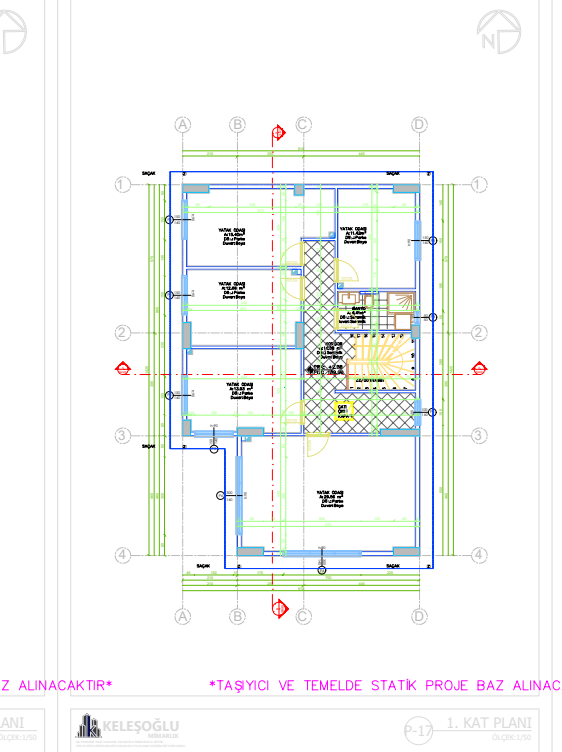

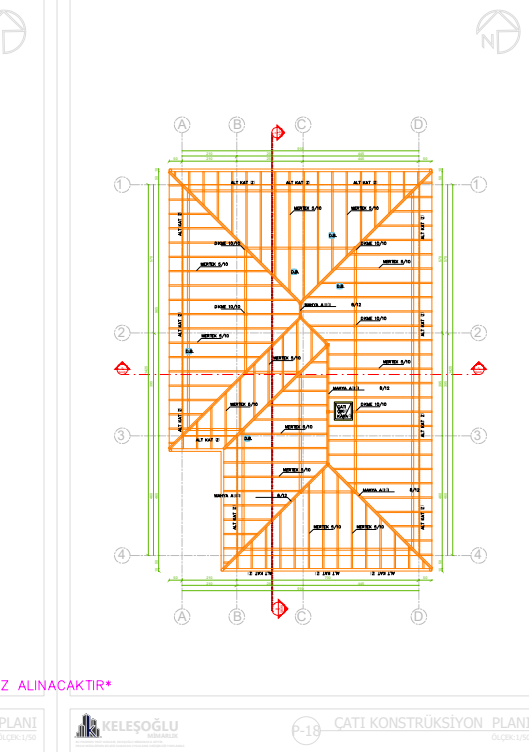

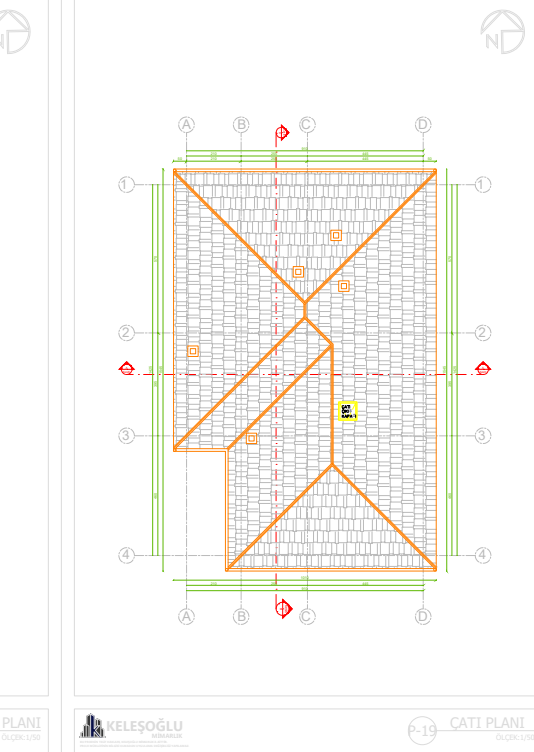

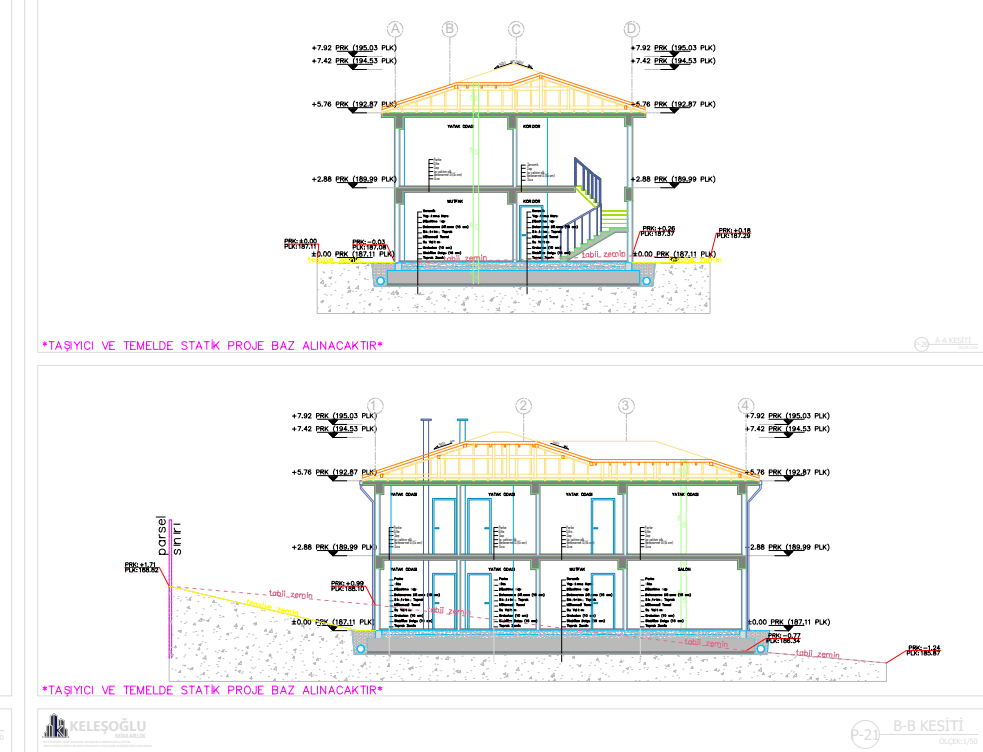

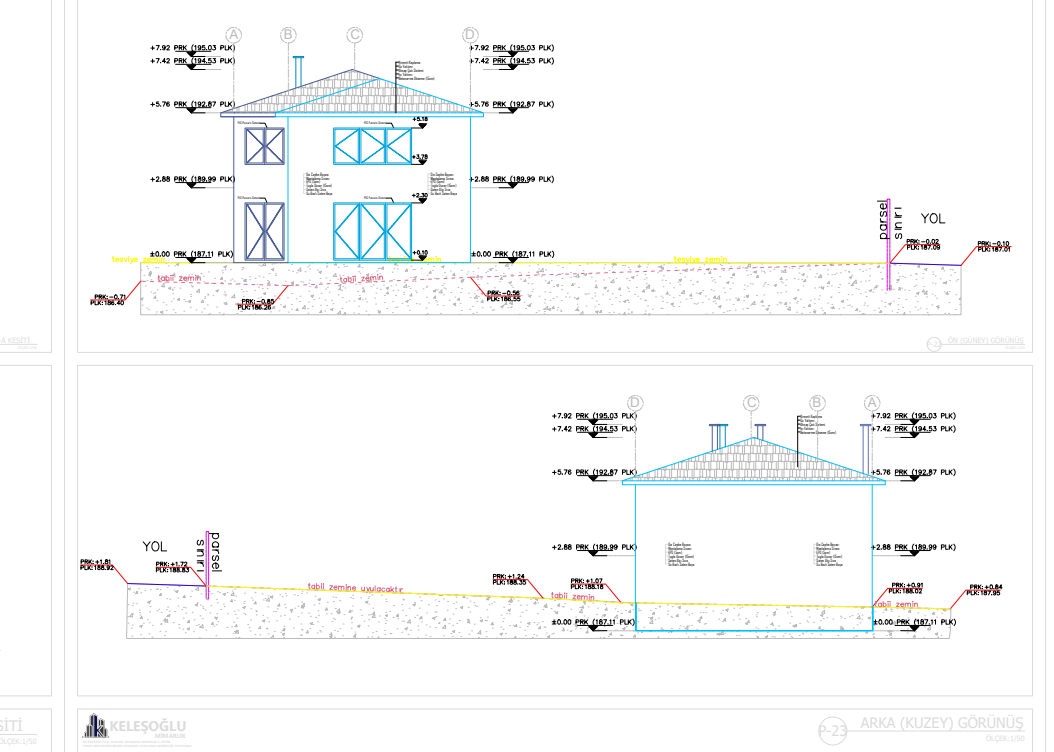

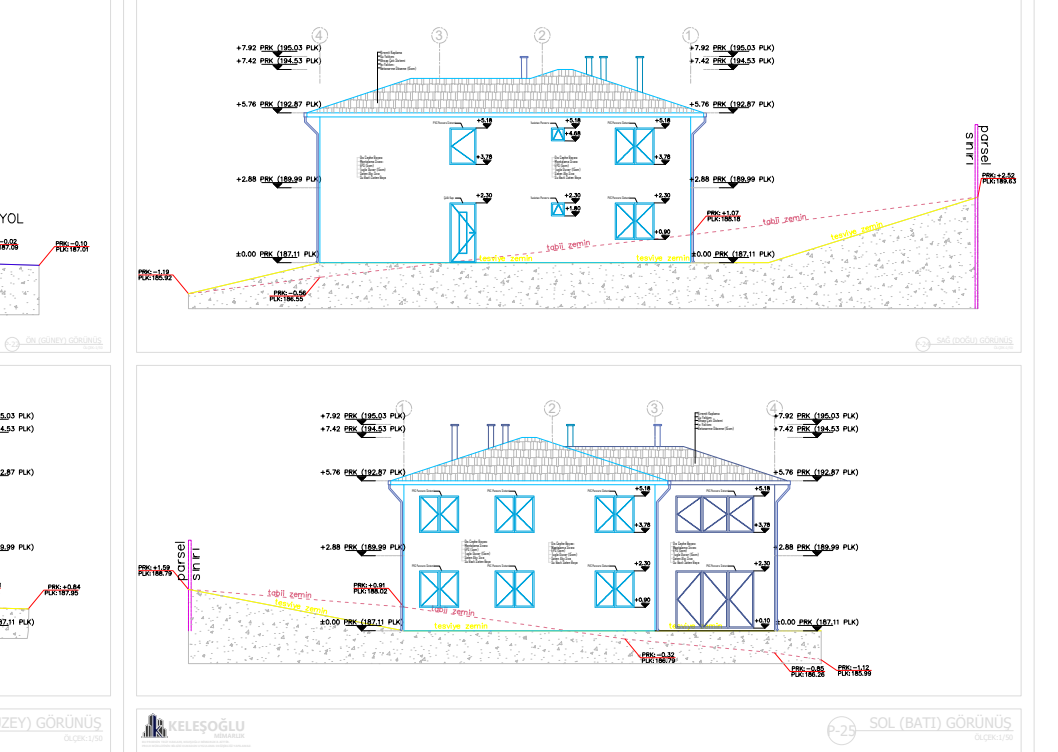

POZ İŞARETLEMESİ

Her çizimin altına, o çizimde görünen imalatların keşif özetindeki poz numaraları yazılmıştır. Çizimin kendisine dokunulmamıştır: işaretleme paftanın boş alanına yapılmış, onaylı nüsha (41_MIMARI_PROJE.pdf) olduğu gibi bırakılmıştır.

Poz numaraları ve tanımlar keşif özetinden okunmuştur; cetvellerde 55 pozun tamamı yer alır. 15.xxx ve 43.xxx ÇŞB 2026 birim fiyat kitabı, TKDK-xxxx TKDK 17.02.2026 Özel Poz Tablosu, ÖP-15 özel pozdur. Aynı poz birden çok çizimde görünebilir. Elektrik pozları (35.xxx) bu paftada değil, onaylı elektrik projesinde işaretlidir — 43_ELEKTRIK_PROJESI.pdf.

DİKKAT — Foseptiğin ayrı bir detay paftası yoktur; yalnız yerleşim planında görünür. Foseptik betonarme değildir: kazı ve grobeton oturma yatağı üzerine yerleştirilen prefabrik polietilen sızdırmaz tanktır (ÖP-15). Bakıcı evi paftaları için sağdaki cetvelin notuna bakınız.

MUSAB EDER ÇİFTLİĞİ KANATLI (ETLİK PİLİÇ) KÜMESİ
KOCAELİ İLİ KARAMÜRSEL İLÇESİ İNEBEYLİ MAHALLESİ ADA:138 PARSEL:17

P-1 YERLEŞİM PLANI (foseptik dâhil)

Poz No	İmalat
15.120.1001	Makine ile yumuşak ve sert toprak kazılması
15.120.1101	Makine ile her derinlik ve her genişlikte yumuşak ve sert toprak kazılması
15.150.1003	Beton santralinde üretilen veya satın alınan ve beton pompasıyla basılan, C 16/20 basınç dayanım sınıfında, gri renkte, normal hazır beton dökülmesi (beton nakli dahil)
TKDK-0091	Betonarme direkli galvanizli tel örgü çit yapılması (Tip-1)
43.527.1001	Çapı 150 mm HDPE koruge boru döşenmesi (SN 8, lastik conta ve boru bedeli dahil)
15.150.1005	Beton santralinde üretilen veya satın alınan ve beton pompasıyla basılan, C 25/30 basınç dayanım sınıfında, gri renkte, normal hazır beton dökülmesi (beton nakli dahil)
15.180.1003	Plywood ile düz yüzeyli betonarme kalıbı yapılması
15.160.1003	Ø 8 - Ø 12 mm nervürlü beton çelik çubuğu, çubukların kesilmesi, bükülmesi ve yerine konulması
15.560.1003	Betonarme kompozit rögar kapağı temini ve yerine konulması
ÖP-15	Prefabrik polietilen sızdırmaz foseptik tankı — 6 m³, rotasyon kalıplı, temini, yerine konulması ve giriş-çıkış bağlantılarının yapılması
35.100.1104	Ana dağıtım panosu (dikili tip galvanizli sac, en az 700 mm en, 400 mm derinlik) (%25 müteahhit kârı dahil)
35.100.2106	Sayaç panosu (sıva üstü galvanizli sac tablo, 0,50-0,60 m²) (%25 müteahhit kârı dahil)
35.135.3201	Üç fazlı zaman tarifeli elektronik aktif sayaç, en az 5(100) A, 3x230/400 V (%25 müteahhit kârı dahil)
35.110.1104	Termik-manyetik kompakt şalter 3x160 A, Icu 35 kA — ana giriş (%25 müteahhit kârı dahil)
35.115.1003	Kaçak akım koruma şalteri 2x63 A, 30 mA (%25 müteahhit kârı dahil)
35.140.3105	YVV (NYY) 1 kV yeraltı kablosu ile besleme hattı tesisi — 1x35 mm² (%25 müteahhit kârı dahil)
35.140.3101	YVV (NYY) 1 kV yeraltı kablosu ile besleme hattı tesisi — 1x6 mm² (%25 müteahhit kârı dahil)
35.172.1706	Aydınlatma direği — taban çapı en az 80 mm, yükseklik en az 4,00 m (%25 müteahhit kârı dahil)
35.170.4002	LED projektör, ışık akısı en az 5100 lm (%25 müteahhit kârı dahil)

P-2 KÜMES A VE B BLOK ZEMİN KAT PLANI

Poz No	İmalat
15.120.1001	Makine ile yumuşak ve sert toprak kazılması
15.150.1003	Beton santralinde üretilen veya satın alınan ve beton pompasıyla basılan, C 16/20 basınç dayanım sınıfında, gri renkte, normal hazır beton dökülmesi (beton nakli dahil)
15.150.1005	Beton santralinde üretilen veya satın alınan ve beton pompasıyla basılan, C 25/30 basınç dayanım sınıfında, gri renkte, normal hazır beton dökülmesi (beton nakli dahil)
15.180.1003	Plywood ile düz yüzeyli betonarme kalıbı yapılması
15.160.1003	Ø 8 - Ø 12 mm nervürlü beton çelik çubuğu, çubukların kesilmesi, bükülmesi ve yerine konulması
15.160.1004	Ø 14 - Ø 28 mm nervürlü beton çelik çubuğu, çubukların kesilmesi, bükülmesi ve yerine konulması
15.160.1002	Nervürlü çelik hasırın yerine konulması
15.225.1010	20 cm kalınlığındaki teçhizatsız gazbeton duvar blokları ile duvar yapılması (gazbeton tutkalı ile)
15.225.1410	20 cm kalınlığındaki teçhizatlı gazbeton lento temini ve yerine konulması
15.225.1004	10 cm kalınlığındaki teçhizatsız gazbeton duvar blokları ile duvar yapılması (gazbeton tutkalı ile)
15.275.1116	250 kg çimento dozlu harç ile kaba sıva yapılması
15.275.1117	200 kg çimento ve kireç karışımı harç ile kaba sıva yapılması (iç cephe)
15.540.1606	Brüt beton, sıvalı veya eski boyalı yüzeylere astar uygulanarak silikon esaslı su bazlı dış cephe boyası yapılması
15.540.1537	Yeni sıva yüzeylere astar uygulanarak iki kat su bazlı plastik antibakteriyel iç cephe boyası yapılması
TKDK-0177	(25x70 - 25x75 - 40x80 cm) anma ebatlarında, her türlü desen ve yüzey özelliğinde, renkli duvar karosu ile 3 mm derz aralıklı döşeme, duvar ve cephe kaplaması yapılması (karo yapıştırıcısı ile)
TKDK-0151	5 cm poliüretan dolgulu (üst 0,50 mm düz, alt 0,40 mm düz) fabrikasyon rulo boyama sistemi ile boyanmış galvaniz levhalar ile ısı yalıtımlı kapı yapılması
TKDK-0175	PVC kaplamalı, iki yüzü odun lifinden yapılmış levhalarla (MDF) presli, kraft dolgulu iç kapı kanadı yapılması, yerinde takılması
15.550.1002	1,50 mm kalınlığında sıcak haddelenmiş sacdan bükme kapı kasası yapılması ve yerine konulması
43.527.1001	Çapı 150 mm HDPE koruge boru döşenmesi (SN 8, lastik conta ve boru bedeli dahil)

Elektrik pozları (35.xxx) bu paftada değil, onaylı elektrik projesinde işaretlidir — 43_ELEKTRIK_PROJESI.pdf.

P-3 · P-4 KÜMES A VE B BLOK KESİTLERİ

Poz No	İmalat
15.120.1001	Makine ile yumuşak ve sert toprak kazılması
15.150.1003	Beton santralinde üretilen veya satın alınan ve beton pompasıyla basılan, C 16/20 basınç dayanım sınıfında, gri renkte, normal hazır beton dökülmesi (beton nakli dahil)
15.150.1005	Beton santralinde üretilen veya satın alınan ve beton pompasıyla basılan, C 25/30 basınç dayanım sınıfında, gri renkte, normal hazır beton dökülmesi (beton nakli dahil)
15.180.1003	Plywood ile düz yüzeyli betonarme kalıbı yapılması
15.160.1003	Ø 8 - Ø 12 mm nervürlü beton çelik çubuğu, çubukların kesilmesi, bükülmesi ve yerine konulması
15.160.1004	Ø 14 - Ø 28 mm nervürlü beton çelik çubuğu, çubukların kesilmesi, bükülmesi ve yerine konulması
15.160.1002	Nervürlü çelik hasırın yerine konulması
15.165.1003	Her çeşit profil, çelik çubuk ve çelik saclarla karkas (çerçeve) inşaat yapılması, yerine tespiti (boya bedeli hariç)
TKDK-0042	6 cm poliüretan dolgulu (üst min. 0,40 mm, alt min. 0,30 mm) boyalı galvanizli sac levhalar ile ısı yalıtımlı çatı kaplaması yapılması
15.225.1010	20 cm kalınlığındaki teçhizatsız gazbeton duvar blokları ile duvar yapılması (gazbeton tutkalı ile)
15.225.1410	20 cm kalınlığındaki teçhizatlı gazbeton lento temini ve yerine konulması
15.275.1116	250 kg çimento dozlu harç ile kaba sıva yapılması
15.275.1117	200 kg çimento ve kireç karışımı harç ile kaba sıva yapılması (iç cephe)
15.550.1202	Lama ve profil demirlerden çeşitli demir işleri yapılması ve yerine konulması
TKDK-0115	Galvanizli düz sacdan yağmur oluğu veya iniş borusu yapılması
15.315.1001	Ø 70 mm çapında bir ucu muflu sert PVC yağmur borusu temini ve yerine tesbiti

Elektrik pozları (35.xxx) bu paftada değil, onaylı elektrik projesinde işaretlidir — 43_ELEKTRIK_PROJESI.pdf.

P-5 · P-6 KÜMES A BLOK GÖRÜNÜŞLERİ

Poz No	İmalat
TKDK-0042	6 cm poliüretan dolgulu (üst min. 0,40 mm, alt min. 0,30 mm) boyalı galvanizli sac levhalar ile ısı yalıtımlı çatı kaplaması yapılması
15.275.1116	250 kg çimento dozlu harç ile kaba sıva yapılması
15.540.1606	Brüt beton, sıvalı veya eski boyalı yüzeylere astar uygulanarak silikon esaslı su bazlı dış cephe boyası yapılması
15.550.1202	Lama ve profil demirlerden çeşitli demir işleri yapılması ve yerine konulması
TKDK-0115	Galvanizli düz sacdan yağmur oluğu veya iniş borusu yapılması
15.315.1001	Ø 70 mm çapında bir ucu muflu sert PVC yağmur borusu temini ve yerine tesbiti
TKDK-0151	5 cm poliüretan dolgulu (üst 0,50 mm düz, alt 0,40 mm düz) fabrikasyon rulo boyama sistemi ile boyanmış galvaniz levhalar ile ısı yalıtımlı kapı yapılması
15.165.1003	Her çeşit profil, çelik çubuk ve çelik saclarla karkas (çerçeve) inşaat yapılması, yerine tespiti (boya bedeli hariç)

Elektrik pozları (35.xxx) bu paftada değil, onaylı elektrik projesinde işaretlidir — 43_ELEKTRIK_PROJESI.pdf.

P-7 · P-8 KÜMES A VE B BLOK ÖN VE ARKA GÖRÜNÜŞLERİ

Poz No	İmalat
TKDK-0042	6 cm poliüretan dolgulu (üst min. 0,40 mm, alt min. 0,30 mm) boyalı galvanizli sac levhalar ile ısı yalıtımlı çatı kaplaması yapılması
15.275.1116	250 kg çimento dozlu harç ile kaba sıva yapılması
15.540.1606	Brüt beton, sıvalı veya eski boyalı yüzeylere astar uygulanarak silikon esaslı su bazlı dış cephe boyası yapılması
15.550.1202	Lama ve profil demirlerden çeşitli demir işleri yapılması ve yerine konulması
TKDK-0115	Galvanizli düz sacdan yağmur oluğu veya iniş borusu yapılması
15.315.1001	Ø 70 mm çapında bir ucu muflu sert PVC yağmur borusu temini ve yerine tesbiti
TKDK-0151	5 cm poliüretan dolgulu (üst 0,50 mm düz, alt 0,40 mm düz) fabrikasyon rulo boyama sistemi ile boyanmış galvaniz levhalar ile ısı yalıtımlı kapı yapılması
15.165.1003	Her çeşit profil, çelik çubuk ve çelik saclarla karkas (çerçeve) inşaat yapılması, yerine tespiti (boya bedeli hariç)

Elektrik pozları (35.xxx) bu paftada değil, onaylı elektrik projesinde işaretlidir — 43_ELEKTRIK_PROJESI.pdf.

P-9 · P-10 KÜMES B BLOK GÖRÜNÜŞLERİ

Poz No	İmalat
TKDK-0042	6 cm poliüretan dolgulu (üst min. 0,40 mm, alt min. 0,30 mm) boyalı galvanizli sac levhalar ile ısı yalıtımlı çatı kaplaması yapılması
15.275.1116	250 kg çimento dozlu harç ile kaba sıva yapılması
15.540.1606	Brüt beton, sıvalı veya eski boyalı yüzeylere astar uygulanarak silikon esaslı su bazlı dış cephe boyası yapılması
15.550.1202	Lama ve profil demirlerden çeşitli demir işleri yapılması ve yerine konulması
TKDK-0115	Galvanizli düz sacdan yağmur oluğu veya iniş borusu yapılması
15.315.1001	Ø 70 mm çapında bir ucu muflu sert PVC yağmur borusu temini ve yerine tesbiti
TKDK-0151	5 cm poliüretan dolgulu (üst 0,50 mm düz, alt 0,40 mm düz) fabrikasyon rulo boyama sistemi ile boyanmış galvaniz levhalar ile ısı yalıtımlı kapı yapılması
15.165.1003	Her çeşit profil, çelik çubuk ve çelik saclarla karkas (çerçeve) inşaat yapılması, yerine tespiti (boya bedeli hariç)

Elektrik pozları (35.xxx) bu paftada değil, onaylı elektrik projesinde işaretlidir — 43_ELEKTRIK_PROJESI.pdf.

P-11 GÜBRE ÇUKURU

Poz No	İmalat
15.120.1101	Makine ile her derinlik ve her genişlikte yumuşak ve sert toprak kazılması
15.150.1003	Beton santralinde üretilen veya satın alınan ve beton pompasıyla basılan, C 16/20 basınç dayanım sınıfında, gri renkte, normal hazır beton dökülmesi (beton nakli dahil)
15.150.1005	Beton santralinde üretilen veya satın alınan ve beton pompasıyla basılan, C 25/30 basınç dayanım sınıfında, gri renkte, normal hazır beton dökülmesi (beton nakli dahil)
15.180.1003	Plywood ile düz yüzeyli betonarme kalıbı yapılması
15.160.1003	Ø 8 - Ø 12 mm nervürlü beton çelik çubuğu, çubukların kesilmesi, bükülmesi ve yerine konulması
15.160.1004	Ø 14 - Ø 28 mm nervürlü beton çelik çubuğu, çubukların kesilmesi, bükülmesi ve yerine konulması

P-12 · P-13 ÖLÜ ATMA ÇUKURU · YAĞMUR SUYU DEPOSU

Poz No	İmalat
15.120.1101	Makine ile her derinlik ve her genişlikte yumuşak ve sert toprak kazılması
15.150.1003	Beton santralinde üretilen veya satın alınan ve beton pompasıyla basılan, C 16/20 basınç dayanım sınıfında, gri renkte, normal hazır beton dökülmesi (beton nakli dahil)
15.150.1005	Beton santralinde üretilen veya satın alınan ve beton pompasıyla basılan, C 25/30 basınç dayanım sınıfında, gri renkte, normal hazır beton dökülmesi (beton nakli dahil)
15.180.1003	Plywood ile düz yüzeyli betonarme kalıbı yapılması
15.160.1003	Ø 8 - Ø 12 mm nervürlü beton çelik çubuğu, çubukların kesilmesi, bükülmesi ve yerine konulması

P-14 · P-15 SU DEPOSU · SİLO

Poz No	İmalat
15.120.1101	Makine ile her derinlik ve her genişlikte yumuşak ve sert toprak kazılması
15.150.1003	Beton santralinde üretilen veya satın alınan ve beton pompasıyla basılan, C 16/20 basınç dayanım sınıfında, gri renkte, normal hazır beton dökülmesi (beton nakli dahil)
15.150.1005	Beton santralinde üretilen veya satın alınan ve beton pompasıyla basılan, C 25/30 basınç dayanım sınıfında, gri renkte, normal hazır beton dökülmesi (beton nakli dahil)
15.180.1003	Plywood ile düz yüzeyli betonarme kalıbı yapılması
15.160.1003	Ø 8 - Ø 12 mm nervürlü beton çelik çubuğu, çubukların kesilmesi, bükülmesi ve yerine konulması

P-16 … P-25 BAKICI EVİ — ZEMİN VE 1. KAT PLANLARI, ÇATI, KESİTLER VE GÖRÜNÜŞLER

Poz No	İmalat
Bakıcı evi (120 m² x 2 kat = 240 m²) bu paftalarda çizilidir ancak KEŞİF ÖZETİNDE, METRAJ CETVELİNDE VE MALİYET BELGELERİNDE YER ALMAZ. Yatırım kapsamına alınacaksa metrajı çıkarılıp uygun olmayan harcama olarak A3.4-EK'e ve yapım işleri proformasına eklenmelidir; alınmayacaksa mimari projeden çıkarılmalıdır. Rehber, parseldeki bütün yapıların ruhsatlı olmasını zorunlu tutar.	