


MAKİNE-EKİPMAN YERLEŞİM PLANI

MUSAB EDER ÇİFTLİĞİ KANATLI (ETLİK PİLİÇ) KÜMESİ
KOCAELİ İLİ KARAMÜRSEL İLÇESİ İNEBEYLİ MAHALLESİ ADA:138 PARSEL:17

Ölçek 1:300 · Kümes A ve B blok özdeşdir
İç ölçü 78,55 x 13,50 m = 1.060,42 m²

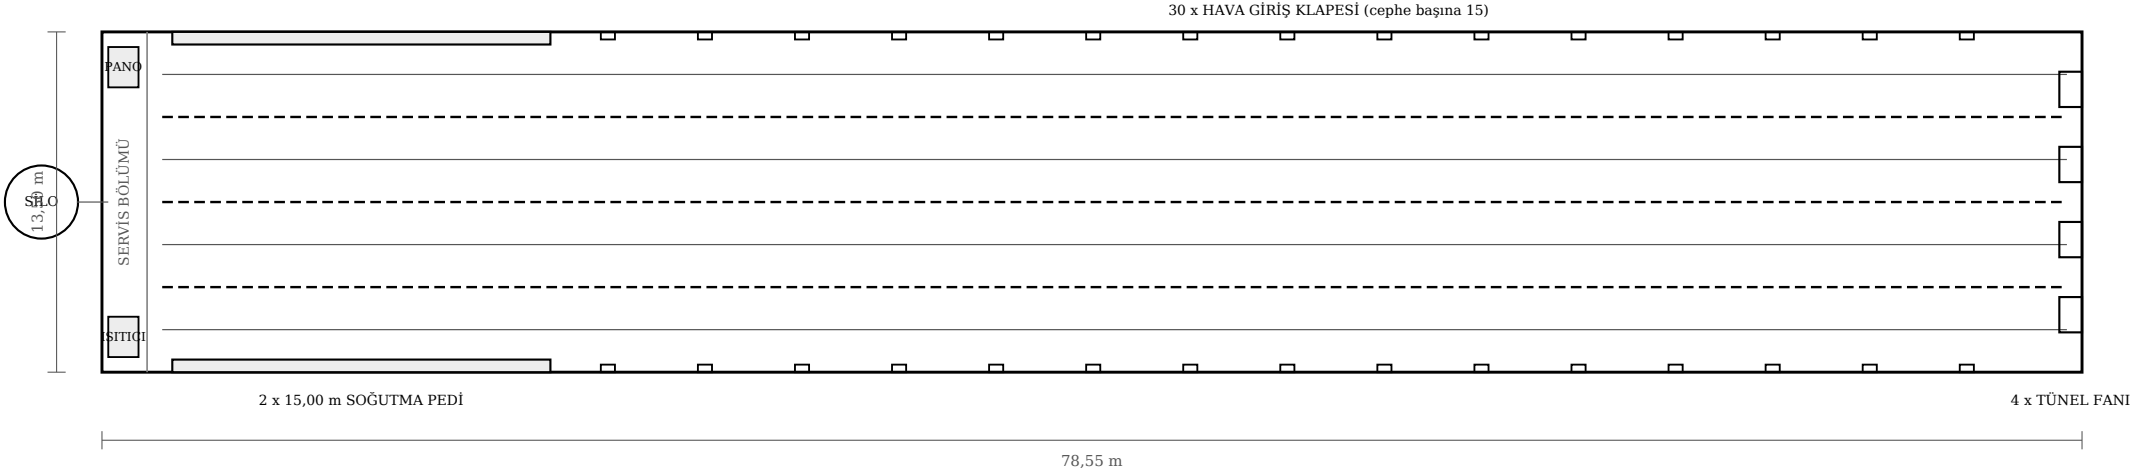

Kümes başına makine-ekipman

Yemleme sistemi	3 hat	Sulama sistemi (nipel)	4 hat	Tünel havalandırma fanı	4 adet
Hava giriş klapesi	30 adet	Soğutma pedi	2 x 15,00 m	Yem silosu	1 adet
Kümes kontrol panosu	1 adet	Sıcak hava üretici (ısıtma)	1 adet		

Adetler makine-ekipman teknik şartnamesi (07), ihtiyaç listesi (12), proforma istek listesi (37) ve teknik proje (44) ile aynıdır; hepsi tek kaynaktan üretilir.
Bu çizim ekipmanın yerleşim düzenini ve adedini gösterir; mimari pafta yerine geçmez. Proje müellifi onaylı paftaya bu düzeni işler.