KELEŞOĞLU MİMARLIK
tel: 0544 453 59 61 | email:kelesoglumimarlikk@gmail.com | adres: ilimtepe mah. 18. sokak no:2 körfez/kocaeli

MUSAB EDER - MİMARİ PROJESİ

Ruhsat Veren Kurum KARAMÜRSEL BELEDİYESİ			İli KOCAELİ		İlçesi KARAMÜRSEL	
Ruhsat Veriliş Maksadı YENİ YAPI	Ruhsat Tarihi	Ruhsat Numarası	Köyü/Mah. İNEBEYLİ	Pafta No. G23-D-11-B-3	Ada No. 138	Parsel No. 17
İmar Durumu Tarihi	İmar Durumu Numarası		Isınma Türü		Yakıt Türü	
Tapu Tescil Belgesi Veren Kurum			Tapu Tescil Belgesi Tarihi		Tapu Tescil Belgesi Numarası	

YAPI SAHİBİNİN		YAPI MÜTEAHHİDİNİN	
Adı Soyadı / Unvanı MUSAB EDER		Adı Soyadı / Unvanı	Kurum Sicil numarası
Bağlı Olduğu Vergi Dairesi	Vergi Dairesi Sicil Numarası	Bağlı Olduğu Vergi Dairesi	Vergi Dairesi Sicil Numarası
Adresi KARAMÜRSEL/KOCAELİ		Adresi	

İNŞAAT ALANI		Ünite Sayısı	Yüz Ölçümü	Yol Seviyesi Altında Kat Sayısı	Yol Seviyesi Üstünde Kat Sayısı	Toplam Kat Sayısı	Yapının Yüksekliği	1 m² sinin Maliyeti	Yapı Sınıfı	Yapı Grubu
KÜMES A BLOK	ZEMİN KAT		1106 m²	0	1	1	4.50 m		2	A
	1. KAT									
	TOPLAM		1106 m²							
KÜMES B BLOK	ZEMİN KAT		1106 m²	0	1	1	4.50 m		2	A
	1. KAT									
	TOPLAM		1106 m²							
GÜBRE ÇUKURU	BODRUM KAT		115 m²	1	0	1	2.70 m		1	B
	TOPLAM		115 m²							
ÖLÜ ATMA ÇUKURU	BODRUM KAT		18 m²	1	0	1	3.00 m		1	B
	TOPLAM		18 m²							
BAKICI EVİ	BODRUM KAT			0	2	2	5.76 m		3	A
	ZEMİN KAT		120 m²							
	1. KAT		120 m²							
	TOPLAM		240 m²							
FOSEPTİK	BODRUM KAT		4 m²	1	0	1	2.50 m		1	B
	TOPLAM		4 m²							
YAĞMUR SUYU DEPOSU	BODRUM KAT		9 m²	1	0	1	3.00 m		1	C
	TOPLAM		9 m²							
SİLO	BODRUM KAT	2	8.41 m²	0	1	1	5.00 m		1	B
	TOPLAM		16.82 m²							
SU DEPOSU	BODRUM KAT		12 m²	1	0	1	3.00 m		1	C
	TOPLAM		12 m²							
	GENEL TOPLAM		2626.82 m²							

İnşaatın Toplam Maliyeti (Arsa Hariç)	Ait Olduğu Yıl 2026	Yapının Arsa Değeri	Toplam Maliyet (Arsa Dahil)
İskeletin Cinsi	İskeletin Dolgu Maddesi	Yığma Yapının Cinsi	

UYARI !

İşe başlamadan evvel bütün ölçüleri şantiyede kontrol edip,farkları ilgililere bildiriniz.

5846 sayılı fikir ve sanat eserleri yasası gereğince bu tasarıma ait bütün haklar proje müellifi mimara aittir.

Bu projedeki taşıyıcı sistem mimari tasarımla bir bütündür. Proje müellifi mimarın haberi ve onayı olmadan projede, projedeki taşıyıcı sistemde ve yapı üzerinde değişiklik yapılamaz, kopya edilemez ve çoğaltılamaz.

MİMAR KAŞE/İMZA

RUHSAT EKİ PROJELER			YAPI DENETİM KURULUŞU
BRANŞI	ADI SOYADI	Oda sicil no. Büro tescil no.	
Mimari Proje	İNCİLAY EZGİ KELEŞOĞLU	91996 41-0987	
Statik Proje			
Tesisat Projesi			
Elektrik Projesi			
Harice taşınacak kazı miktarı :		ŞANTİYE ŞEFİ	Taahhüdü
Kazı malzemesinin taşınacağı yer :			

BELEDİYE ONAYI	ODA VİZESİ
	MİMARİ
MİMARİ PROJENİN,3194 SAYILI İMAR KANUNU VE YÖNETMELİKLERİNE, İMAR DURUMUNA VE RÖPERLİ KROKİSİNE UYGUNLUĞU TARAFIMDAN KONTROL EDİLMİŞTİR.	MİMARİ PROJENİN,3194 SAYILI İMAR KANUNU -YÖNETMELİKLERİNE, İMAR DURUMUNA VE RÖPERLİ KROKİSİNE UYGUNLUĞU TARAFIMDAN KONTROL EDİLMİŞTİR.

SN. MUSAB EDER'E AİT KÜMES VE BAKICI EVİ PROJESİ

İLİ:..KOCAELİ
İLÇESİ:..KARAMÜRSEL
BELEDİYESİ:..KARAMÜRSEL
MAHALLESİ:..İNEBEYLİ
PAFTASI:..G23-D-11-B-3
ADASI:..138
PARSELİ:..17
ALANI:..7966.67 m²

ARSA ALANI	7966.67 M²	
TAKS	–	
KAKS	0.30 + 0.05	
AZAM? TABAN ALANI (TAKS) –		
	KÜMES(A+B)	BAKICI EV?
AZAM? TABAN ALANI (KAKS)	2390 M²	TABAN MAX: 150 M²
PROJEDE TABAN ALANI	1176 M²	120 M²
PROJEDE KAKS'A DAH?L	2352 M²	120 M²

ÇEKME MESAFELER?	
ÖN BAHÇE	10 M
YAN BAHÇE	5 M
ARKA BAHÇE	5 M

1/25000 Ölçekli nazım imar planı hükümlerinin Tarımsal Niteliği Korunacak Alanlar başlıklı plan hükmünde yer alan hmax 6,50 mt (2 kat), e:0.30 değerini aşmayacak şekilde 6.6.2 maddesinde tanımlanan tarımsal amaçlı yapılar yapılabilir." ifadelerinin, "Tarımsal niteliği korunacak alanlar içerisinde belediyesinin uygun görmesi halinde; ilgili kurum ve kuruluşların taşra teşkilatlarının uygun görüşününalınması ve başka bir amaçla kullanılmayacağı hususunda tesis sahiplerince ilgili idareye noterlikçe tasdikli yazılı taahhütte bulunulması şartıyla, hmax 6,50 mt (2 kat), inşaat alanı katsayısı % 30 değerini aşmayacak şekilde 6.6.2maddesinde tanımlanan tarımsal amaçlı yapılarla birlikte inşaat alanı katsayısı %5'den fazla olmayan ve tabanda 75 m² ve 2 kat'ı geçmeyen tarımsal amaçlı bağ evi yapılabilir."

Resmî Gazete'de yayımlanan 04.04.2026 tarihli Tarım Arazilerinin Korunması ve Kullanılmasına Dair Yönetmeliğe göre; "Tarımsal niteliği korunacak alanlar içerisinde; belediyesinin uygun görmesi halinde, ilgili kurum ve kuruluşların taşra teşkilatlarının uygun görüşünün alınması ve başka bir amaçla kullanılmayacağı hususunda tesis sahiplerince ilgili idareye noterlikçe tasdikli yazılı taahhütte bulunulması şartıyla, yönetmeliğin 11.9 maddesinde tanımlanan kanatlı hayvancılık tesisleri (kümes) yapılabilir. Bu kapsamda; kanatlı hayvancılık tesisinin kapalı alanına bağlı olarak, 750 m² ile 1500 m² arasında olması durumunda taban alanı 75 m² ve toplam inşaat alanı 150 m²?yi geçmeyen, 1500 m²?nin üzerinde olması durumunda ise taban alanı 150 m² ve toplam inşaat alanı 300 m²?yi geçmeyen bakıcı evi yapılabilir.

TAKS HESABI= BAKICI EVİ TABAN ALANI < 150 M²
BAKICI EVİ TABAN ALANI = 120 M² < 150 M² OLDUĞUNDAN TAKS UYGUNDUR.

KAKS HESABI = KÜMES ALANI + BAKICI EVİ ALANI = PARSEL ALANI X (0.30) + PARSEL ALANI X (0.05)
7966.67 X (0.30) + 7966.67 X (0.05) = 2390.0 M² + 398.33 M² = 2788.33 M²

KÜMES (A) 1106.00 M²
KÜMES (B) 1106.00 M²
TOPLAM = 2212 M² < 2390 M² OLDUĞUNDAN KAKS UYGUNDUR.

BAKICI EVİ (ZEMİN KAT) 120 M²
BAKICI EVİ (1.KAT) 120 M²
TOPLAM = 240 M² < 398.33 M² OLDUĞUNDAN KAKS UYGUNDUR.

TOPLAM =2212 M² + 240 M² < 2390 M² +240 M² = 2452 M² < 2788.33 M² OLDUĞUNDAN TOPLAM KAKS UYGUNDUR.

TOPLAM BOZULAN ALAN TABLOSU
A–)KÜMES (A BLOK) : 1106 M²
B–)KÜMES (B BLOK) : 1106 M²
C–)GÜBRE ÇUKURU : 115 M²
D–)ÖLÜ ATMA ÇUKURU : 18 M²
E–)BAKICI EVİ : 120.00 M²
F–)FOSEPTİK : 4.00 M²
G–)YAĞMUR SUYU DEPOSU : 9.00 M²
H–)SU DEPOSU : 12.00 M²
I–)TESİS İÇİ YOL : 745.57 M²

1–)SİLO (A): 8.41 M²
2–)SİLO (B): 8.41 M²

TOPLAM : 3252.39 M²

±0.00 KOTLARI
A–)KÜMES (A BLOK)
±0.00 KOTU =180.45+181.57+180.59+179.26/4= 180.46 ort. kot
B–)KÜMES (B BLOK)
±0.00 KOTU =181.71+183.19+180.75+181.90/4= 181.88 ort. kot
C–)GÜBRE ÇUKURU
±0.00 KOTU =183.59+184.01+183.16+182.87/4= 183.40 ort. kot
D–)ÖLÜ ATMA ÇUKURU
±0.00 KOTU =183.64+183.71+183.38+183.46/4= 183.54 ort. kot
E–)BAKICI EVİ
±0.00 KOTU =188.02+188.18+186.79+186.87+186.55+186.26/6= 187.11 ort. kot
F–)FOSEPTİK
±0.00 KOTU =188.33+188.40+188.66+188.58/4= 188.49 ort. kot
G–)YAĞMUR SUYU DEPOSU
±0.00 KOTU =180.38+180.44+180.25+180.29/4= 180.34 ort. kot
H–)SU DEPOSU
±0.00 KOTU =179.99+180.15+180.35+180.21/4= 180.17 ort. kot

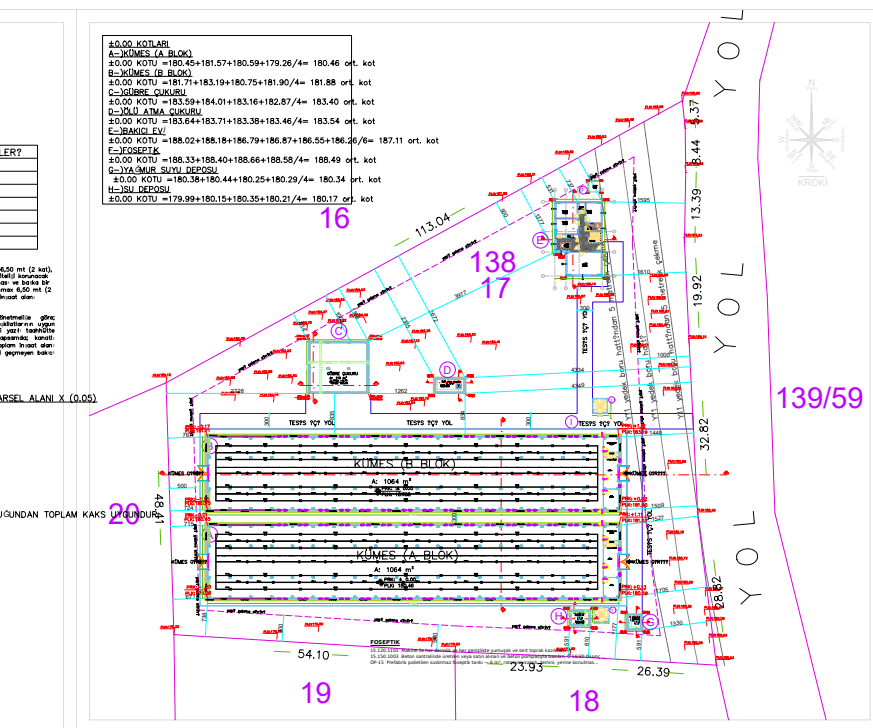

P-1 YERLEŞİM PLANI
ÖLÇEK:1/250

KÜMES A VE B BLOK

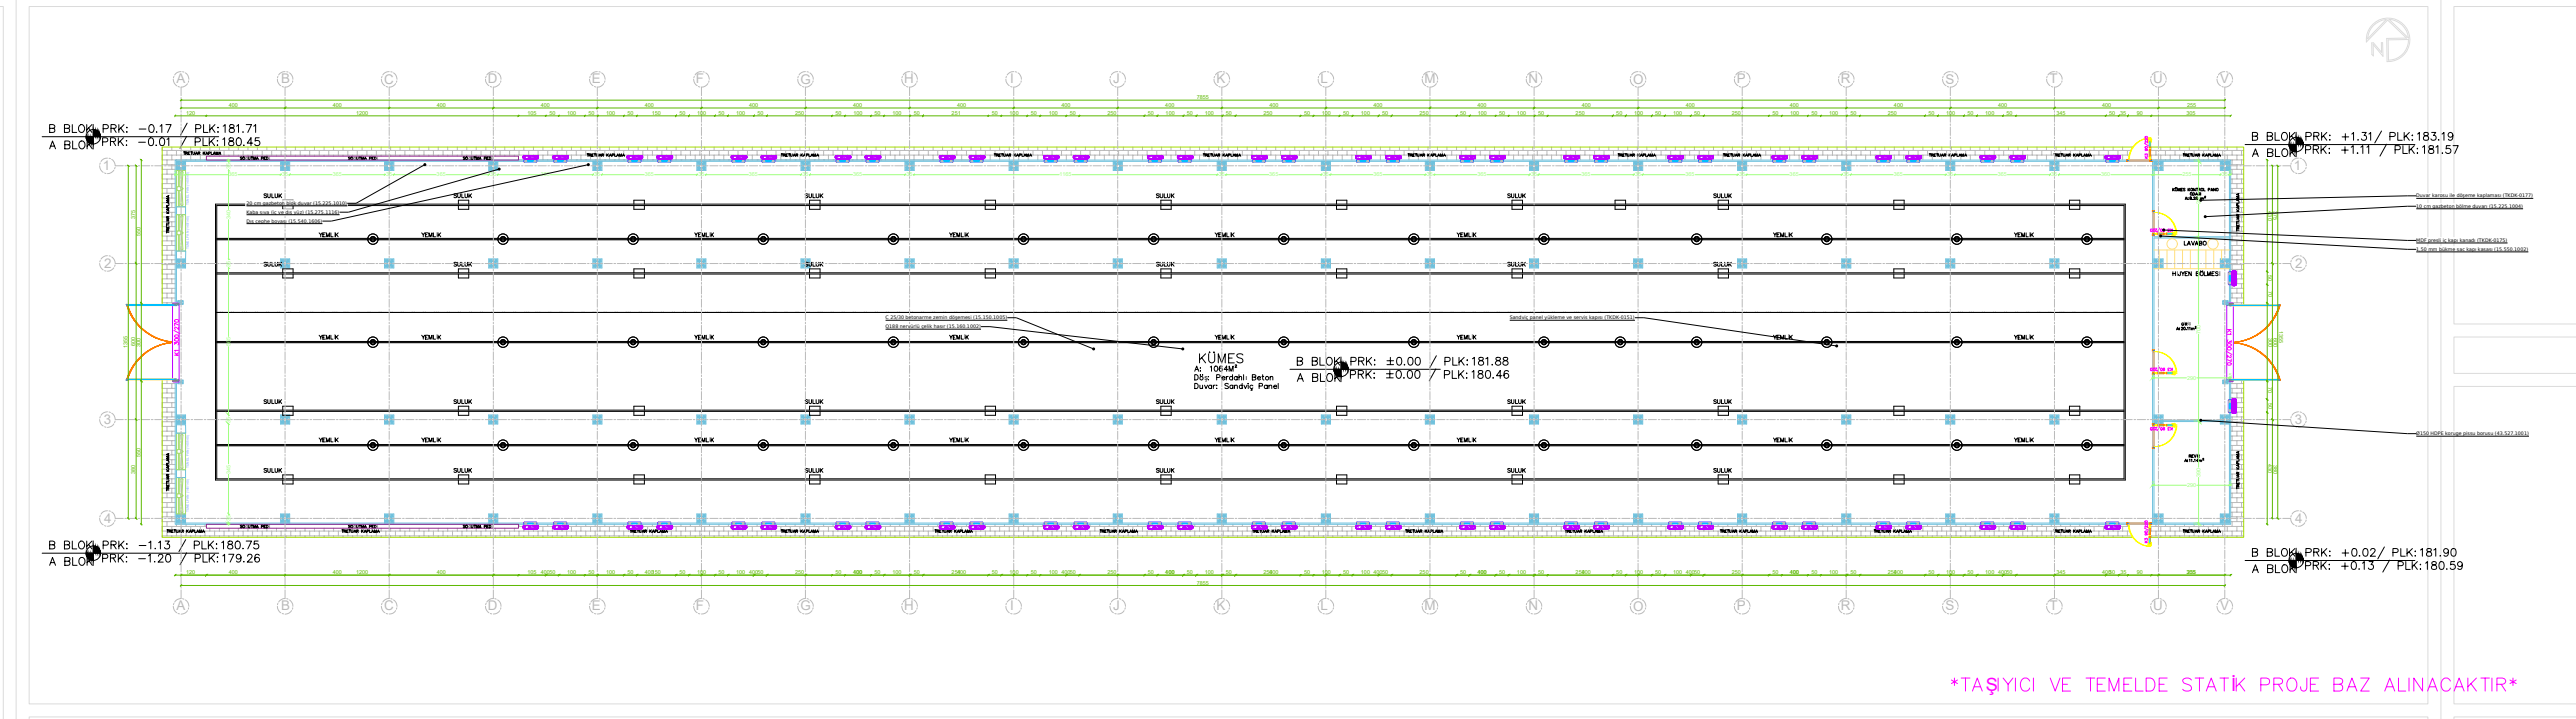
B BLOK PRK: –0.17 / PLK:181.71
A BLOK PRK: –0.02 / PLK:180.43
KÜMES
B BLOK PRK: ±0.00 / PLK:181.88
A BLOK PRK: ±0.00 / PLK:180.46
B BLOK PRK: –1.13 / PLK:180.75
A BLOK PRK: –1.20 / PLK:179.26
B BLOK PRK: +0.02 / PLK:181.90
A BLOK PRK: +0.13 / PLK:180.59

TAŞIYICI VE TEMELDE STATİK PROJE BAZ ALINACAKTIR

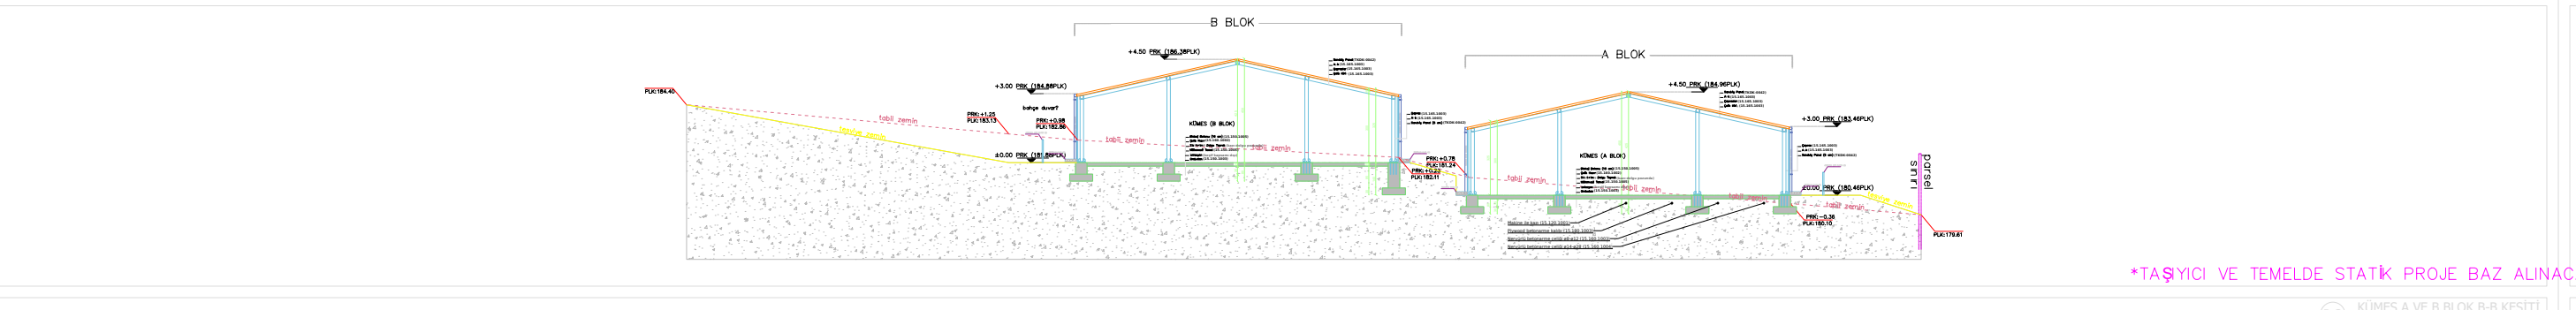

TAŞIYICI VE TEMELDE STATİK PROJE BAZ ALINACAKTIR

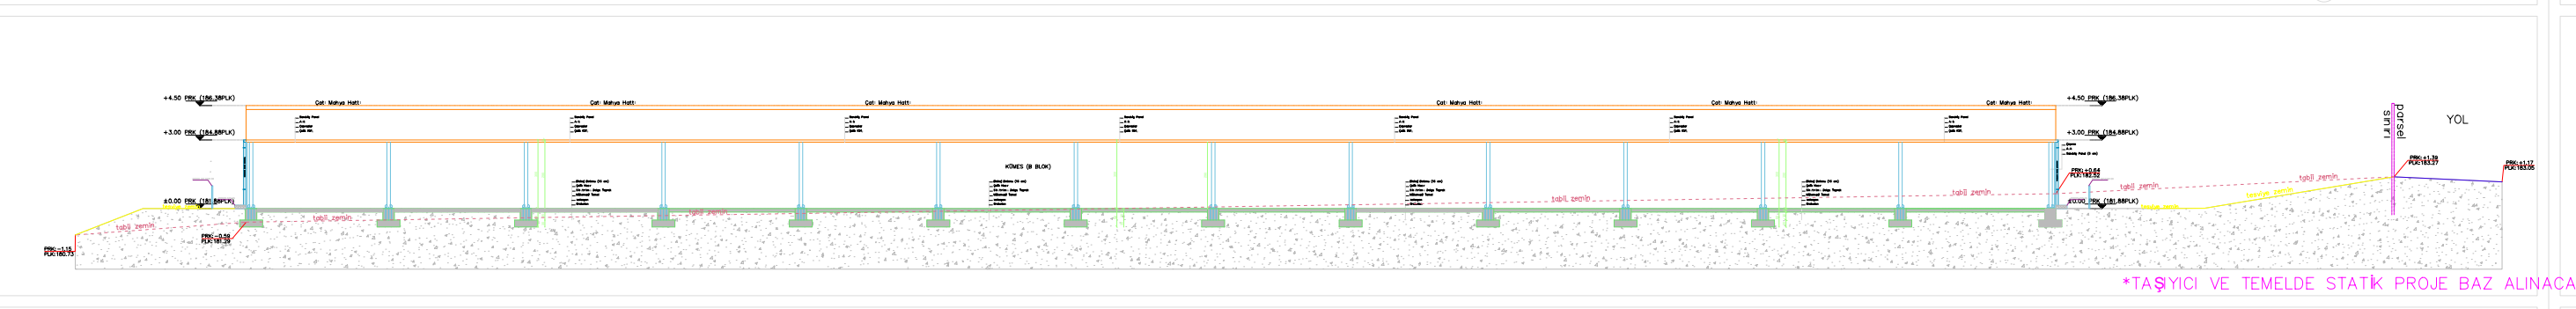

TAŞIYICI VE TEMELDE STATİK PROJE BAZ ALINACAKTIR

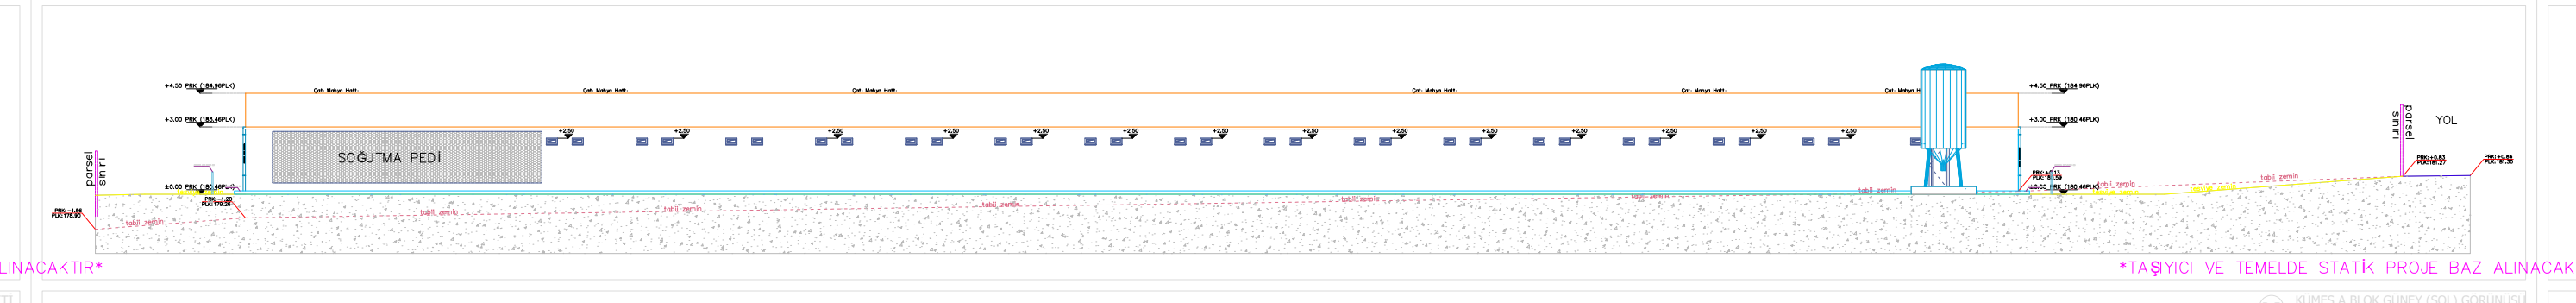

TAŞIYICI VE TEMELDE STATİK PROJE BAZ ALINACAKTIR

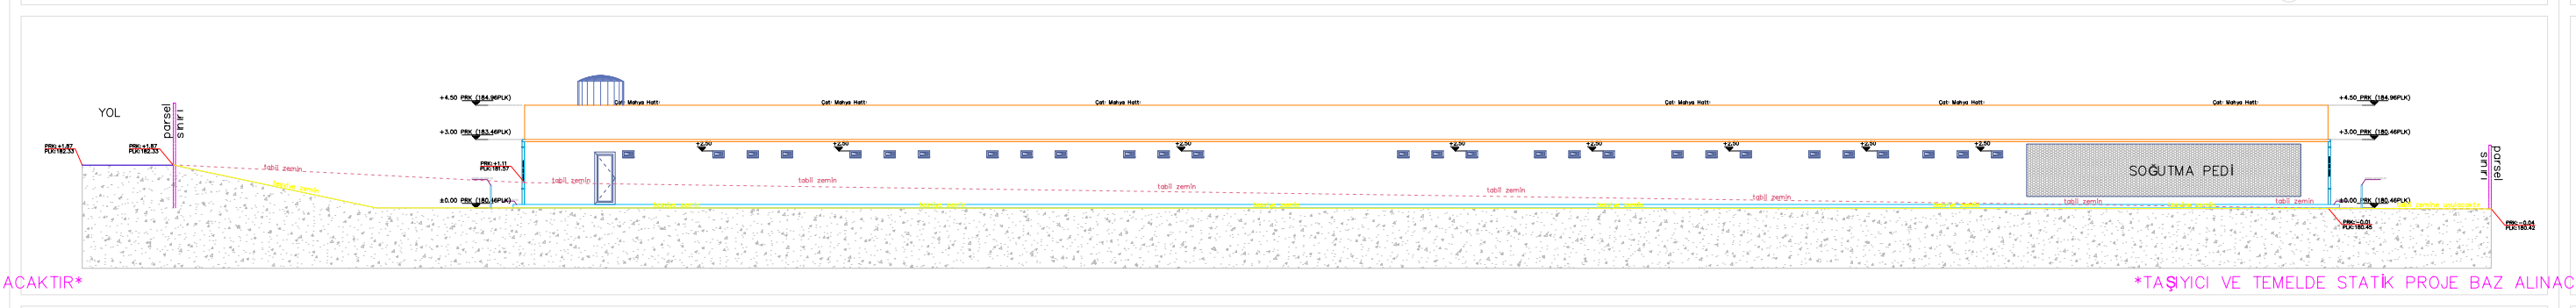

TAŞIYICI VE TEMELDE STATİK PROJE BAZ ALINACAKTIR

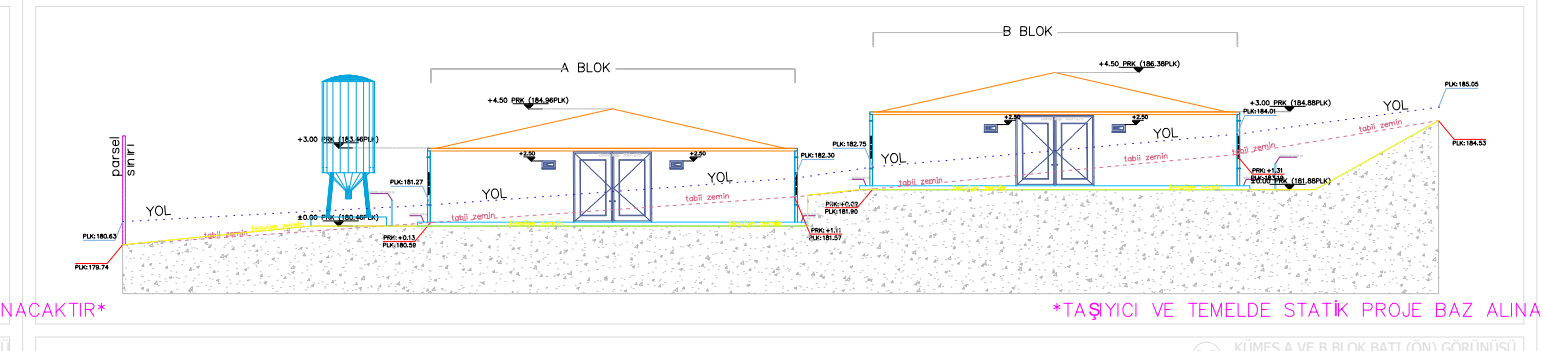

TAŞIYICI VE TEMELDE STATİK PROJE BAZ ALINACAKTIR

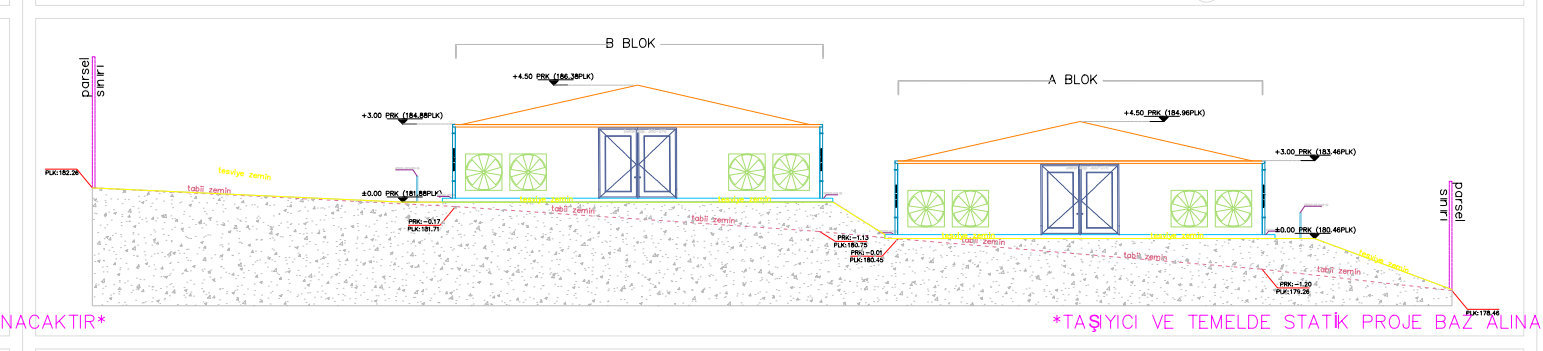

TAŞIYICI VE TEMELDE STATİK PROJE BAZ ALINACAKTIR

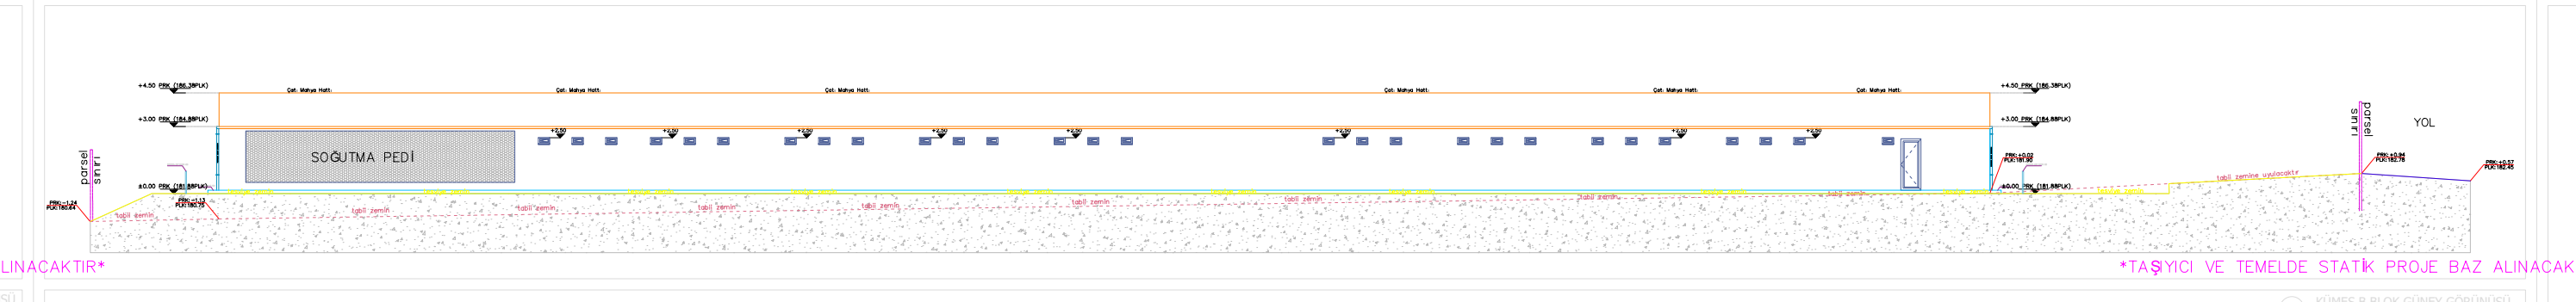

TAŞIYICI VE TEMELDE STATİK PROJE BAZ ALINACAKTIR

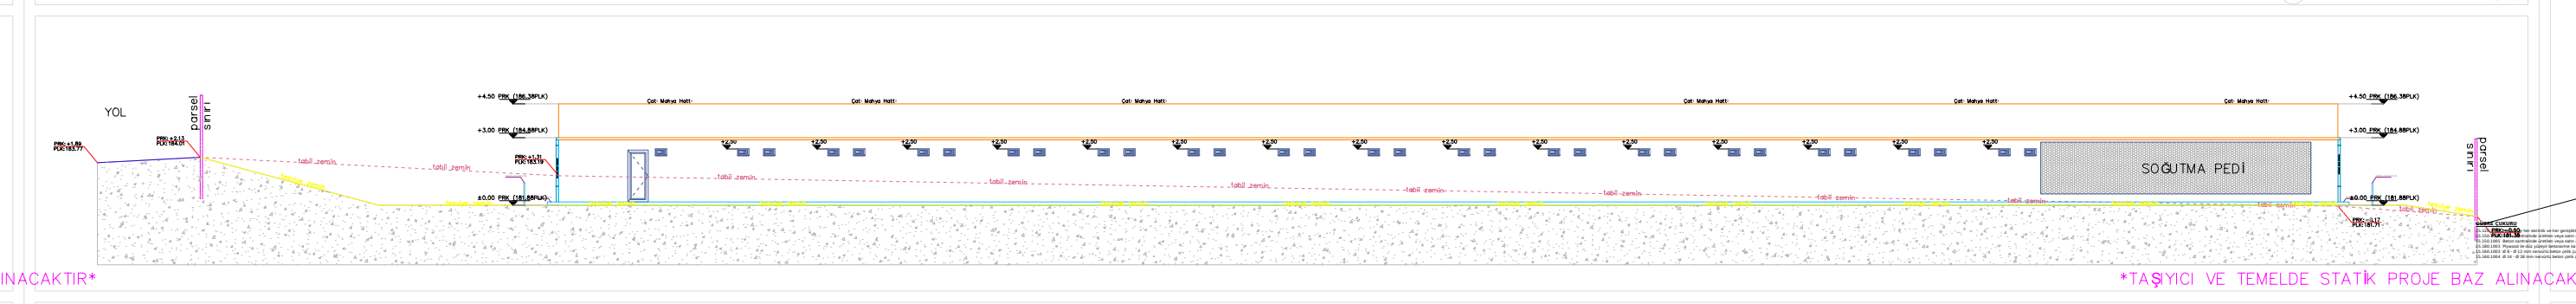

TAŞIYICI VE TEMELDE STATİK PROJE BAZ ALINACAKTIR

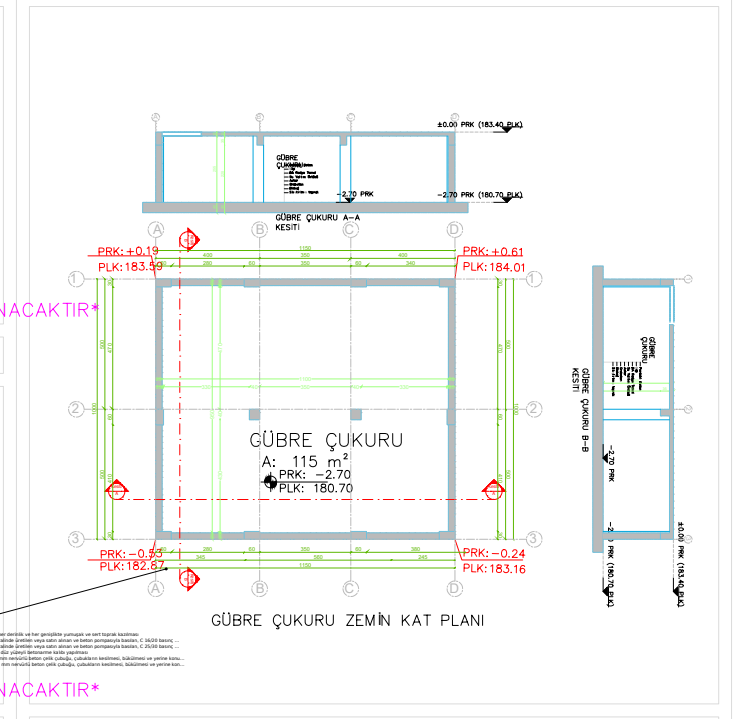

GÜBRE ÇUKURU ZEMİN KAT PLANI

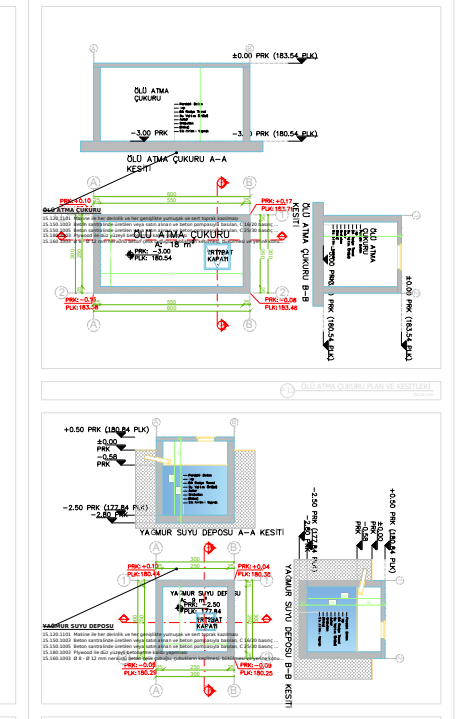

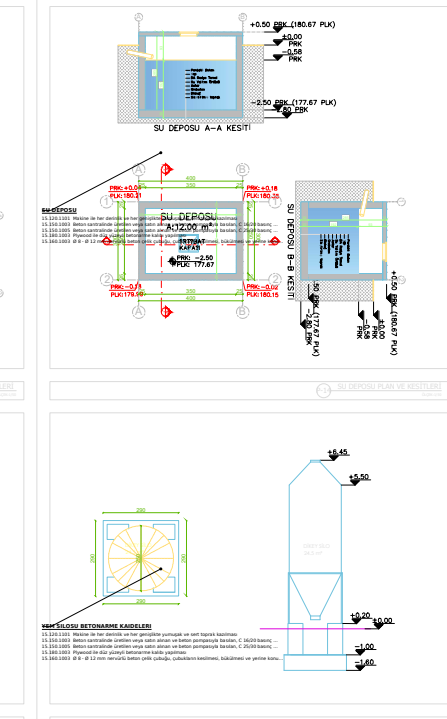

BAKICI EVİ

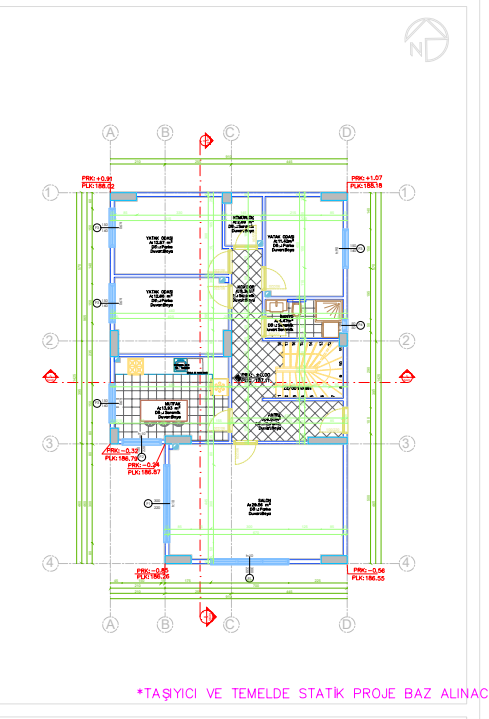

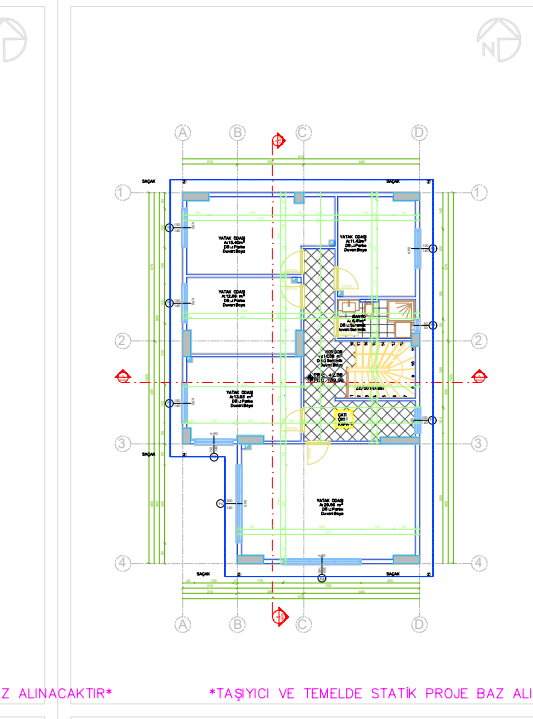

TAŞIYICI VE TEMELDE STATİK PROJE BAZ ALINACAKTIR

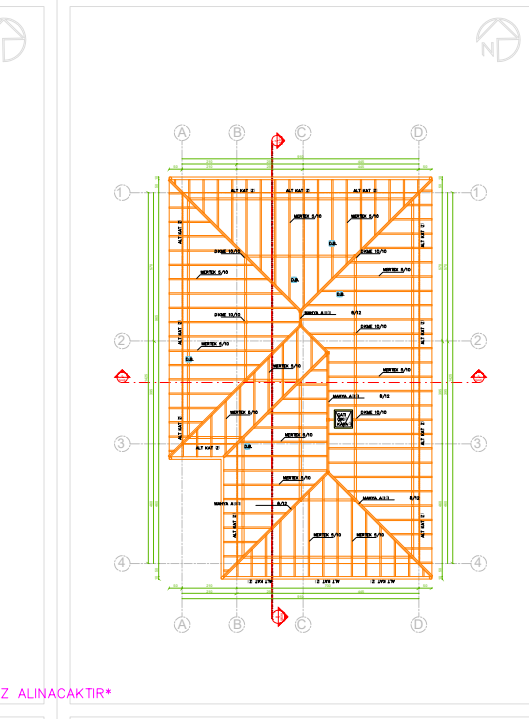

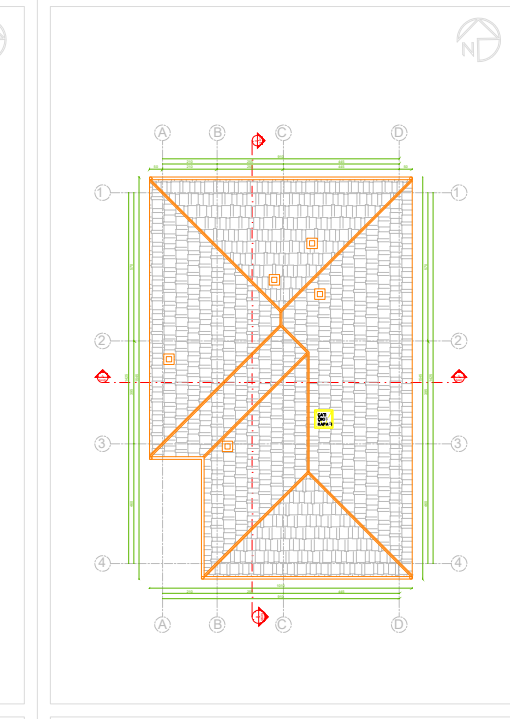

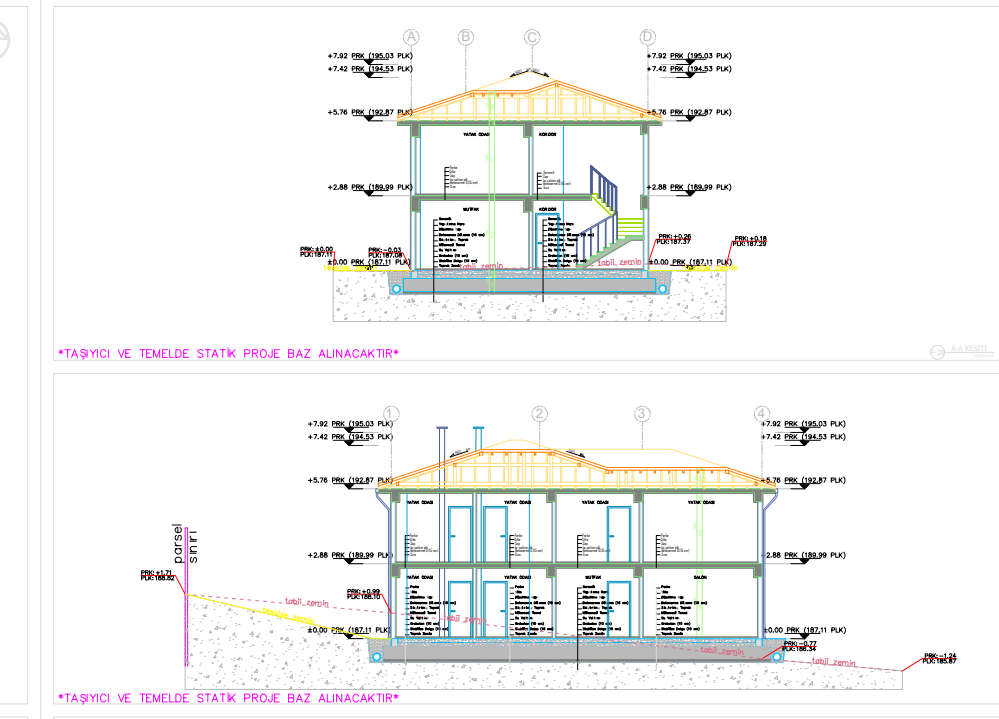

TAŞIYICI VE TEMELDE STATİK PROJE BAZ ALINACAKTIR

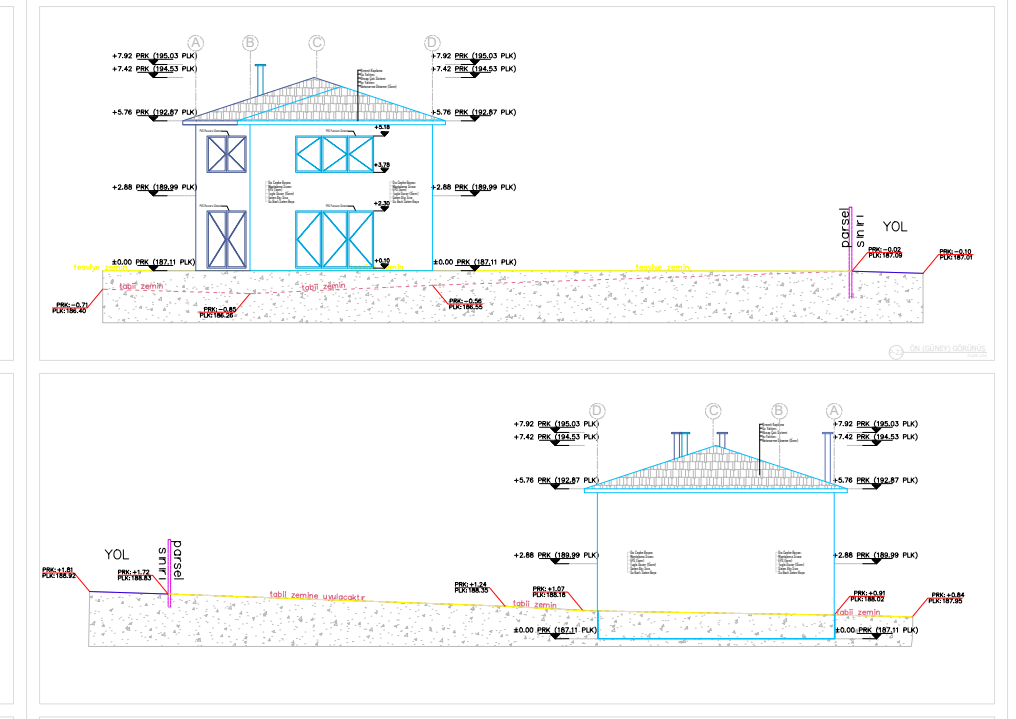

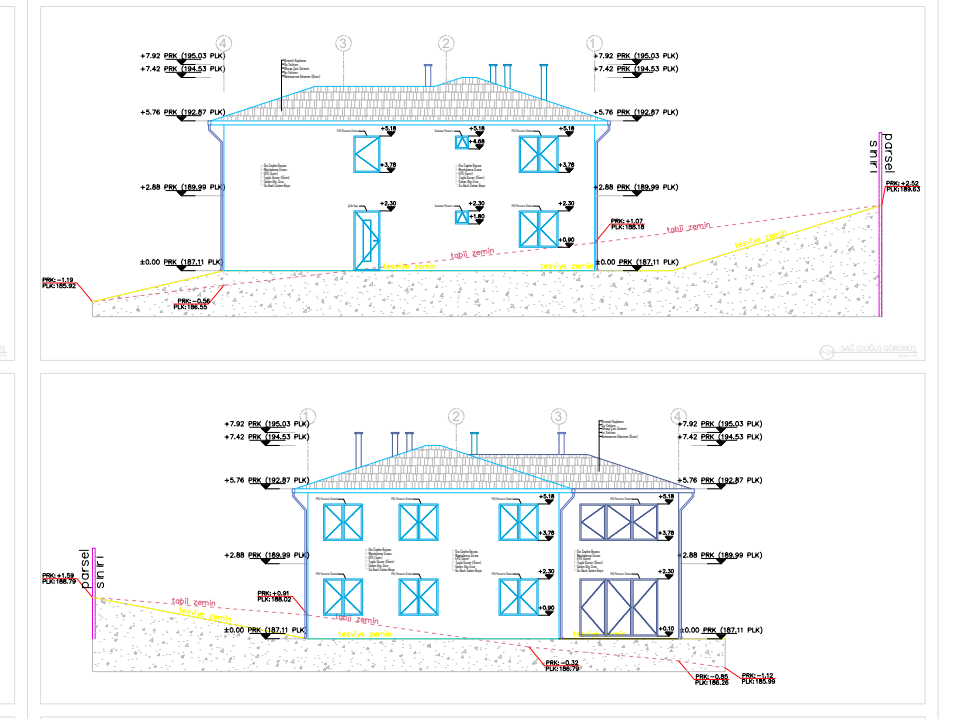

POZ İŞARETLEMESİ

Keşif özetindeki poz numaraları çizimin ilgili yerine işlenmiştir. Mimarın kendi malzeme etiketlerinin (Sandviç Panel, Çelik Hasır, Grobeton...) hemen ardına o katmanın poz numarası yazılmış; mimarın etiketlemediği imalatlara kılavuz çizgili yeni etiket konulmuştur.

Çizimin kendisine dokunulmamıştır: hiçbir çizgi kapatılmamış, işaretleme boş alana yapılmıştır. Onaylı nüsha 41_MIMARI_PROJE.pdf olduğu gibi durur; başvuruya o konur.

Keşifte karşılığı olmayan katmanlar geçiştirilmemiş, gerekçesi yazılmıştır: su yalıtımı ve astar keşif kapsamı dışıdır, sıkıştırılmış dolgu kazı-dolgu pozunun içindedir. Elektrik pozları (35.xxx) mimari paftada değil, onaylı elektrik projesinde gösterilir.

Bakıcı evi paftalarının (P-16...P-25) keşifte, metrajda ve maliyet belgelerinde karşılığı yoktur; foseptiğin ayrı detay paftası yoktur, yalnız yerleşim planında görünür.

MUSAB EDER ÇİFTLİĞİ KANATLI (ETLİK PİLİÇ) KÜMESİ
KOCAELİ İLİ KARAMÜRSEL İLÇESİ İNEBEYLİ MAHALLESİ ADA:138 PARSEL:17