


# MAKİNE-EKİPMAN YERLEŞİM PLANI

MUSAB EDER ÇİFTLİĞİ KANATLI (ETLİK PİLİÇ) KÜMESİ

KOCAELİ İLİ KARAMÜRSEL İLÇESİ İNEBEYLİ MAHALLESİ ADA:138 PARSEL:17

Ölçek 1:300 · Kümes A ve B blok özdeşdir

İç ölçü 78,55 x 13,50 m = 1.060,42 m²

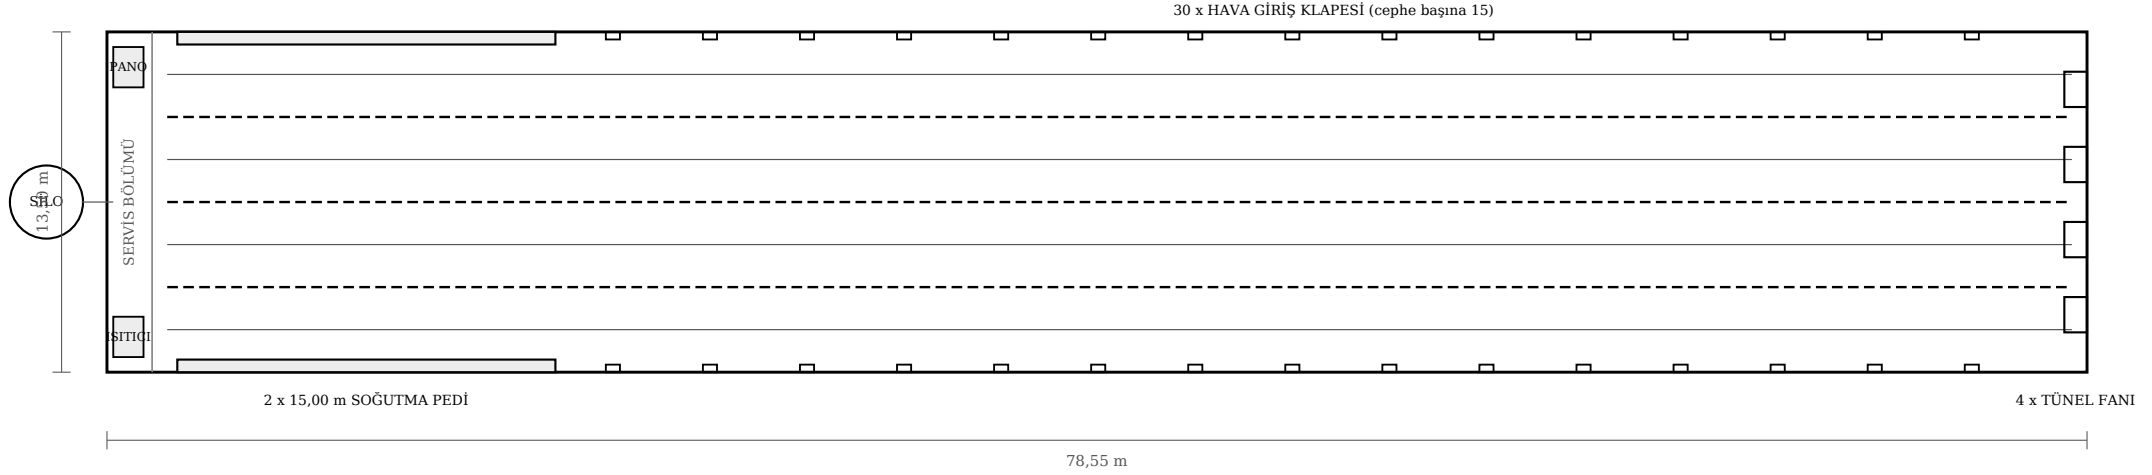

## Kümes başına makine-ekipman

|                                 |                              |                            |         |                             |        |
|---------------------------------|------------------------------|----------------------------|---------|-----------------------------|--------|
| 1 · Yemleme sistemi             | 3 hat                        | 2 · Sulama sistemi (nipel) | 4 hat   | 3 · Tünel havalandırma fanı | 4 adet |
| 4 · Soğutma pedi                | 2 x 15,00 m                  | 5 · Hava giriş klapesi     | 30 adet | 6 · Yem silosu              | 1 adet |
| 7 · Sıcak hava üretici (ısıtma) | 1 adet, en az 264.000 kcal/h | 8 · Kümes kontrol panosu   | 1 adet  |                             |        |

Adetler makine-ekipman teknik şartnamesi (07), ihtiyaç listesi (12), proforma istek listesi (37) ve teknik proje (44) ile aynıdır; hepsi tek kaynaktan üretilir.

Bu çizim ekipmanın yerleşim düzenini ve adedini gösterir; mimari pafta yerine geçmez. Proje müellifi onaylı paftaya bu düzeni işler.